

Спортивно-туристический комплекс
«Нихалоевские Водопады»
по адресу: Чеченская Республика, р-н Шатойский,
с. Нихалой, в границах земельного участка
с кадастровым номером 20:14:4102000:118

РАБОЧАЯ ДОКУМЕНТАЦИЯ

Отопление. Вентиляция. Кондиционирование.

Отдельно-стоящий ресторан

01-00-ОВ2

Согласовано		
Взамен инв. №		
Подп. и дата		
Инв. № подл.		

Изм.	№ док.	Подпись	Дата

Инв. № подл.	Подп. и дата	Взаим. инв. №

ПОЯСНЕНИЯ К ПРОЕКТУ

Рабочие чертежи систем вентиляции и кондиционирования воздуха разработаны на основании:

- утвержденного технического задания;
- архитектурных чертежей;
- действующих нормативных документов:
 - СП 131.13130.2020 - "Строительная климатология";
 - СП 60.13130.2020 - "Отопление, вентиляция и кондиционирование воздуха";

Расчетные параметры наружного воздуха

Холодный период:

- температура -17°С.

Теплый период:

- температура +30°С (для систем вентиляции и кондиционирования воздуха);

Отопление

Теплоснабжение системы отопления осуществляется от отдельностоящей блочной котельной. Теплоноситель вода с параметрами 80/60°С.

Для гидравлической увязки с соседними зданиями пред распределительными коллекторами задания предусмотрена установка балансировочной арматуры. Трубопроводы системы отопления и сшитого полиэтилена (РЕ-Ха) с кислородозащитным слоем.

Разводка трубопроводов осуществляется в стяжке пола.

В качестве отопительных приборов в комнатах применены стальные панельные радиаторы. В ванных комнатах и санузлах применены дизайн-радиаторы из нержавеющей стали, данные радиаторы учтены в разделе АИ.

Вентиляция и кондиционирование воздуха

В здании предусмотрена механическая приточно-вытяжная общеобменная и технологическая вентиляция производственных и административно-бытовых помещений. Для ассимиляции теплоизбытков в залах ресторана предусмотрены системы местного кондиционирования на базе мультисплит-систем. Для предотвращения образования конденсата все воздуховоды теплоизолированы материалом из вспененного каучука.

ОБЩИЕ УКАЗАНИЯ

- Монтаж и сдачу в эксплуатацию систем вентиляции следует производить в соответствии с
 - СП 72.13130 "Внутренние санитарно-технические работы";Все отступления от проектных решений должны быть согласованы с представителями авторского надзора.
- Привязки и отметки трубопроводов и воздухопроводов уточнить при производстве монтажных замеров в натуре с учетом смонтированных строительных конструкций.
- Воздуховоды и детали вентиляционных систем должны быть изготовлены в соответствии с рабочей документацией и утверждены в установленном порядке техническими условиями.
- Присоединение воздухопроводов к технологическому оборудованию должно производиться после его установки.
- Регулирующие приспособления (шибер, дроссель-клапаны, заслонки, регулирующие органы воздухораспределителей) должны легко закрываться и открываться, а также фиксироваться в заданном положении.
- Прокладку фреоновых трубопроводов через стены и перекрытия производить в гильзах. В местах пересечения стен и перекрытий трубопроводами образовавшиеся отверстия и зазоры заделать термоизолирующим материалами на всю глубину ограждения.
- Фреоновые трубопроводы прокладывать в изоляции. Изоляция должна плотно прилегать к поверхности трубопровода. Стыки тщательно проклеить и защитить армированной самоклеющейся лентой.
- Трубопроводы систем теплоснабжения, отопления и холодоснабжения должны быть испытаны гидростатическим или манометрическим методом с соблюдением требований СП 72.13130 и сданы по акту представителям технического надзора до производства теплоизоляционных работ. До испытания и теплоизоляции трубопроводов выполнить врезки и закладные детали устройств для приборов КИП и автоматики.
- Производство работ по монтажу оборудования производить, согласно требованиям производителя..
- Все проходы через противопожарные стены и перегородки должны быть заделаны сертифицированным герметиком. Места расположения противопожарных стен и перегородок смотреть на архитектурных чертежах.
- Все оборудование и материалы должны иметь соответствующие сертификаты РФ.

Ведомость рабочих чертежей основного комплекта ОВ2

Лист	Наименование	Примечания
1	Общие данные	
2	План на отм.+0.000. Отопление	
3	План на отм.+0.000. Вентиляция	
4	План на отм.+3.600. Вентиляция	
5	План на отм.+3.600. Кондиционирование воздуха	

Ведомость ссылочных и прилагаемых документов

Обозначение	Наименование	Примечание
ОВ1-СО	Спецификация оборудования, изделий и материалов	-

Ведомость основных комплектов марки ОВ

Обозначение	Наименование	Примечание
ОВ1	Здание №02	-
ОВ2	Здание №04	
ОВ3	Здание №01	
ОВ4	Здание №05	
ОВ5.1	Здание №06	
ОВ5.2	Здание №07	



Основные показатели по рабочим чертежам комплекта ОВ1

Наименование здания (сооружения), помещения	Объем, м3	Периоды года при tн, °С	Расход теплоты, Вт				Расход холода, Вт	Установле нная мощность электродви гателей, кВт
			на отопление	на вентиляцию	на горячие водоснабжени е	общий		
Здание №04	-	-17	21600	-	см. проект ВК	337500	-	-
	-	+30	-	-	см. проект ВК	-	18100	

						ОВ2						
Изм.	Кол.уч	Лист	№док.	Подпись	Дата	Многофункциональный туристический центр "Нихалойские водопады"						
ГИП						Здание № 04				Стадия	Лист	Листов
Разработал	Слюзов									Р	01	
Норм.контр.						Общие данные						
Инв.№				Дог.№								




Экспликация помещений 1 этажа копия 1			
Номер	Имя	Площадь, м2	Кат. пом.
1.01	Зал ресторана №1	100.4	
1.02	Зал ресторана №2	87.5	
1.03	VIP-комната на 14 мест	27.9	
1.05	Бар ресторана	9.7	
1.06	Склад бара	5.6	B4
1.07	Пом. ЭОМ/СС	8.1	B4
1.08	Коридор	32.8	
1.09	Умывальная	6.7	
1.10	СУ М	2.8	
1.11	СУ Ж	2.5	
1.12	СУ МГ/Ж	4	
1.13	ПТИ	1.6	B4
1.14	Раздевалка Ж	10.6	
1.15	Табури/аутриучная	5.6	
1.16.1	Сервисная (зона моющей столовой посуды)	13.3	B3
1.16.2	Сервисная	9.3	B3
1.17	Гриль-зона	17.8	B3
1.18	Миско-уборный цех	17.8	B3
1.19	Кладовая сухих продуктов	9.2	B4
1.20	Коридор	33.1	
1.21	Окочной цех	20.1	B3
1.22	Кладовая овощей	5	B4
1.23	Кладовая соевых и напитков	5	B4
1.24	Табури	1.7	
1.25	Управление отходов	6.9	B4
1.26	Кладовая и моющая тары	7	B4
1.27	Табури	2.2	
1.28	Зона колдильных камер	18.9	
1.29	Кабинет зав. про-вом	5.9	
1.30	Руководств.	8.1	B4
1.31	Мучной цех	17.8	B3
1.32.1	Производственный цех (холодная зона)	46	B3
1.32.2	Производственный цех (горячая зона)	10.4	B3
1.32.3	Производственный цех (зона мойки крупинок посуды)	7.6	B3
1.35	Кладовая инвентаря	3.8	B4
1.36	Помещение персонала	9.5	B3
1.37	Табури	2	
1.38	ПТИ	2.9	B4
1.39	Пом. ввода ГВС, ХВС	5.5	B4
1.40	СУ М	2.4	
1.41	СУ Ж	2.2	
1.42	Душевая Ж	1.6	
1.43	Душевая М	1.6	
1.44	Раздевалка М	11.1	
1.04	Терраса	226.3	
1.45	Крыльцо	15.6	
1.47	Крыльцо	4	
1.48	Крыльцо	2.4	
1.49	Крыльцо	2.4	
1.50	Крыльцо	2.9	
1.51	Крыльцо	2.4	
1.52	Крыльцо	3.7	
		871.2	

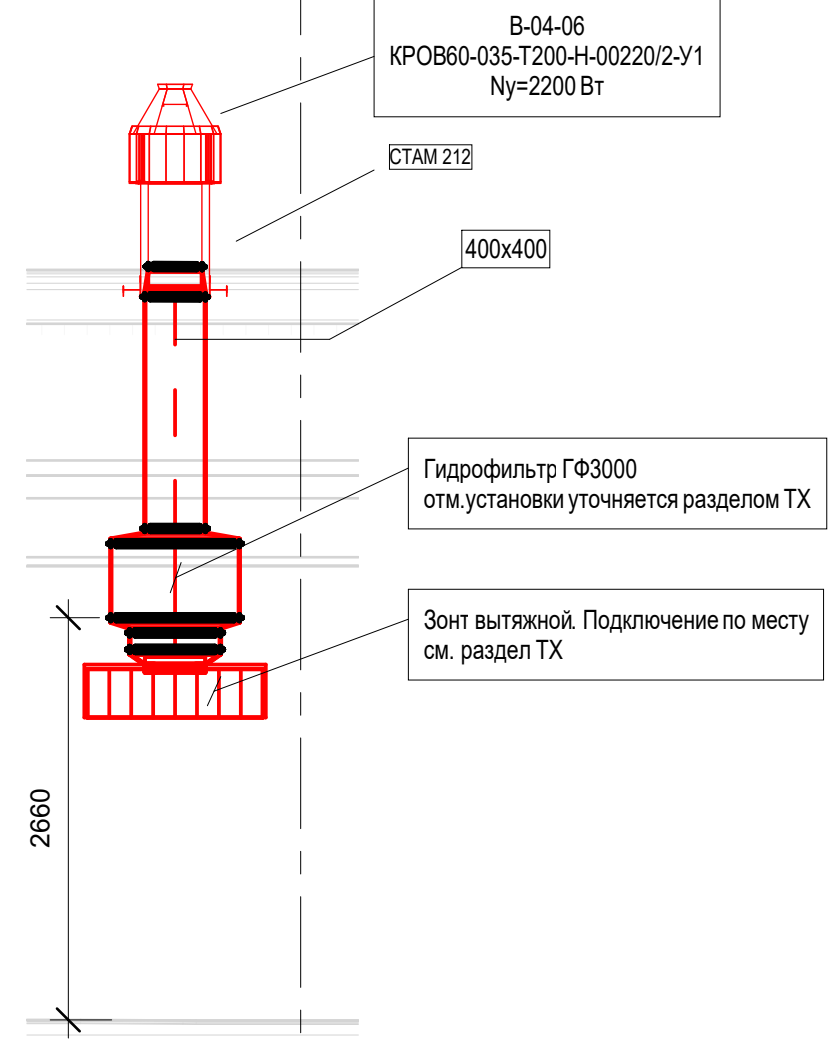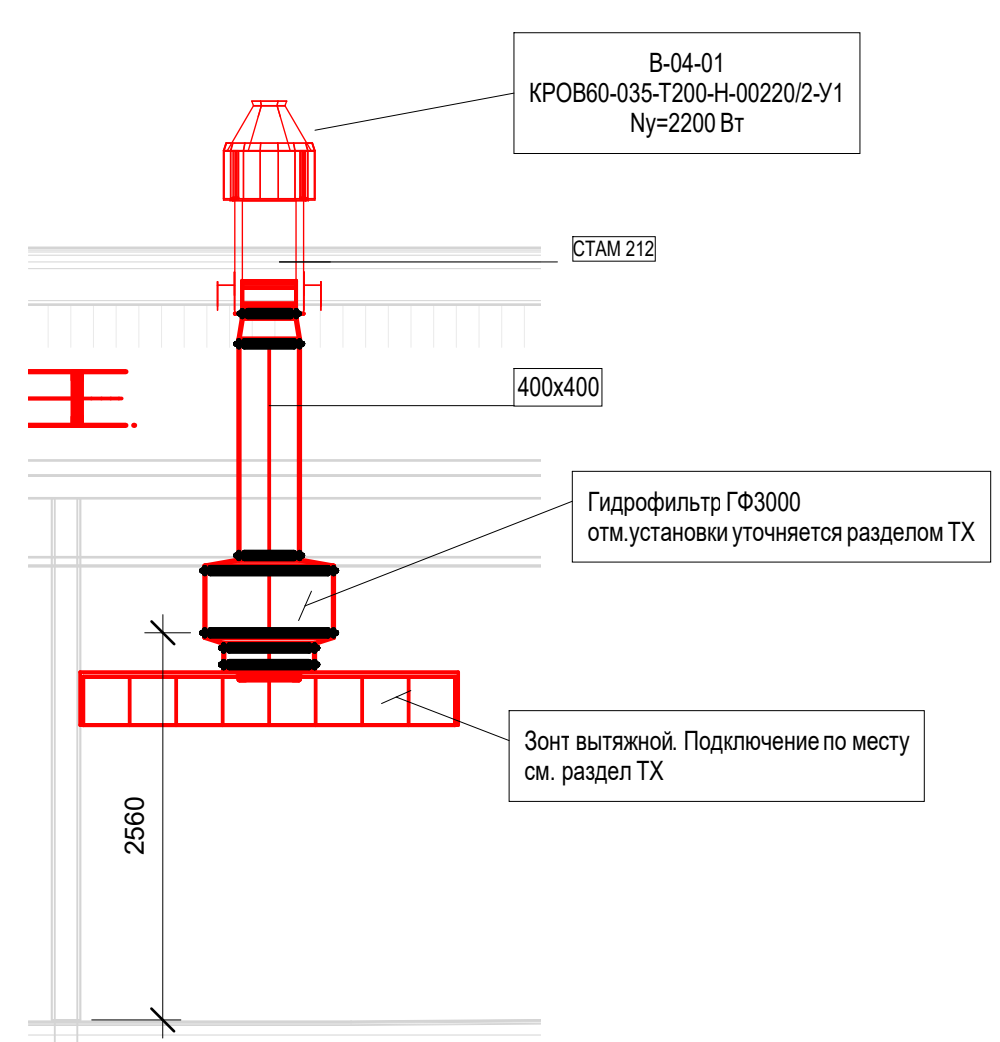

Об2					
Мультифункциональный туристический центр "Некаполюс водопав"					
Здание №04				Старая	Лист
План на отл. +0.000. Разводка воздуховодов				P	03
Формат А0 189 x 841					

Имя № подл.	Согласовано					
	Подп. и дата					
	Взам. инв. №					

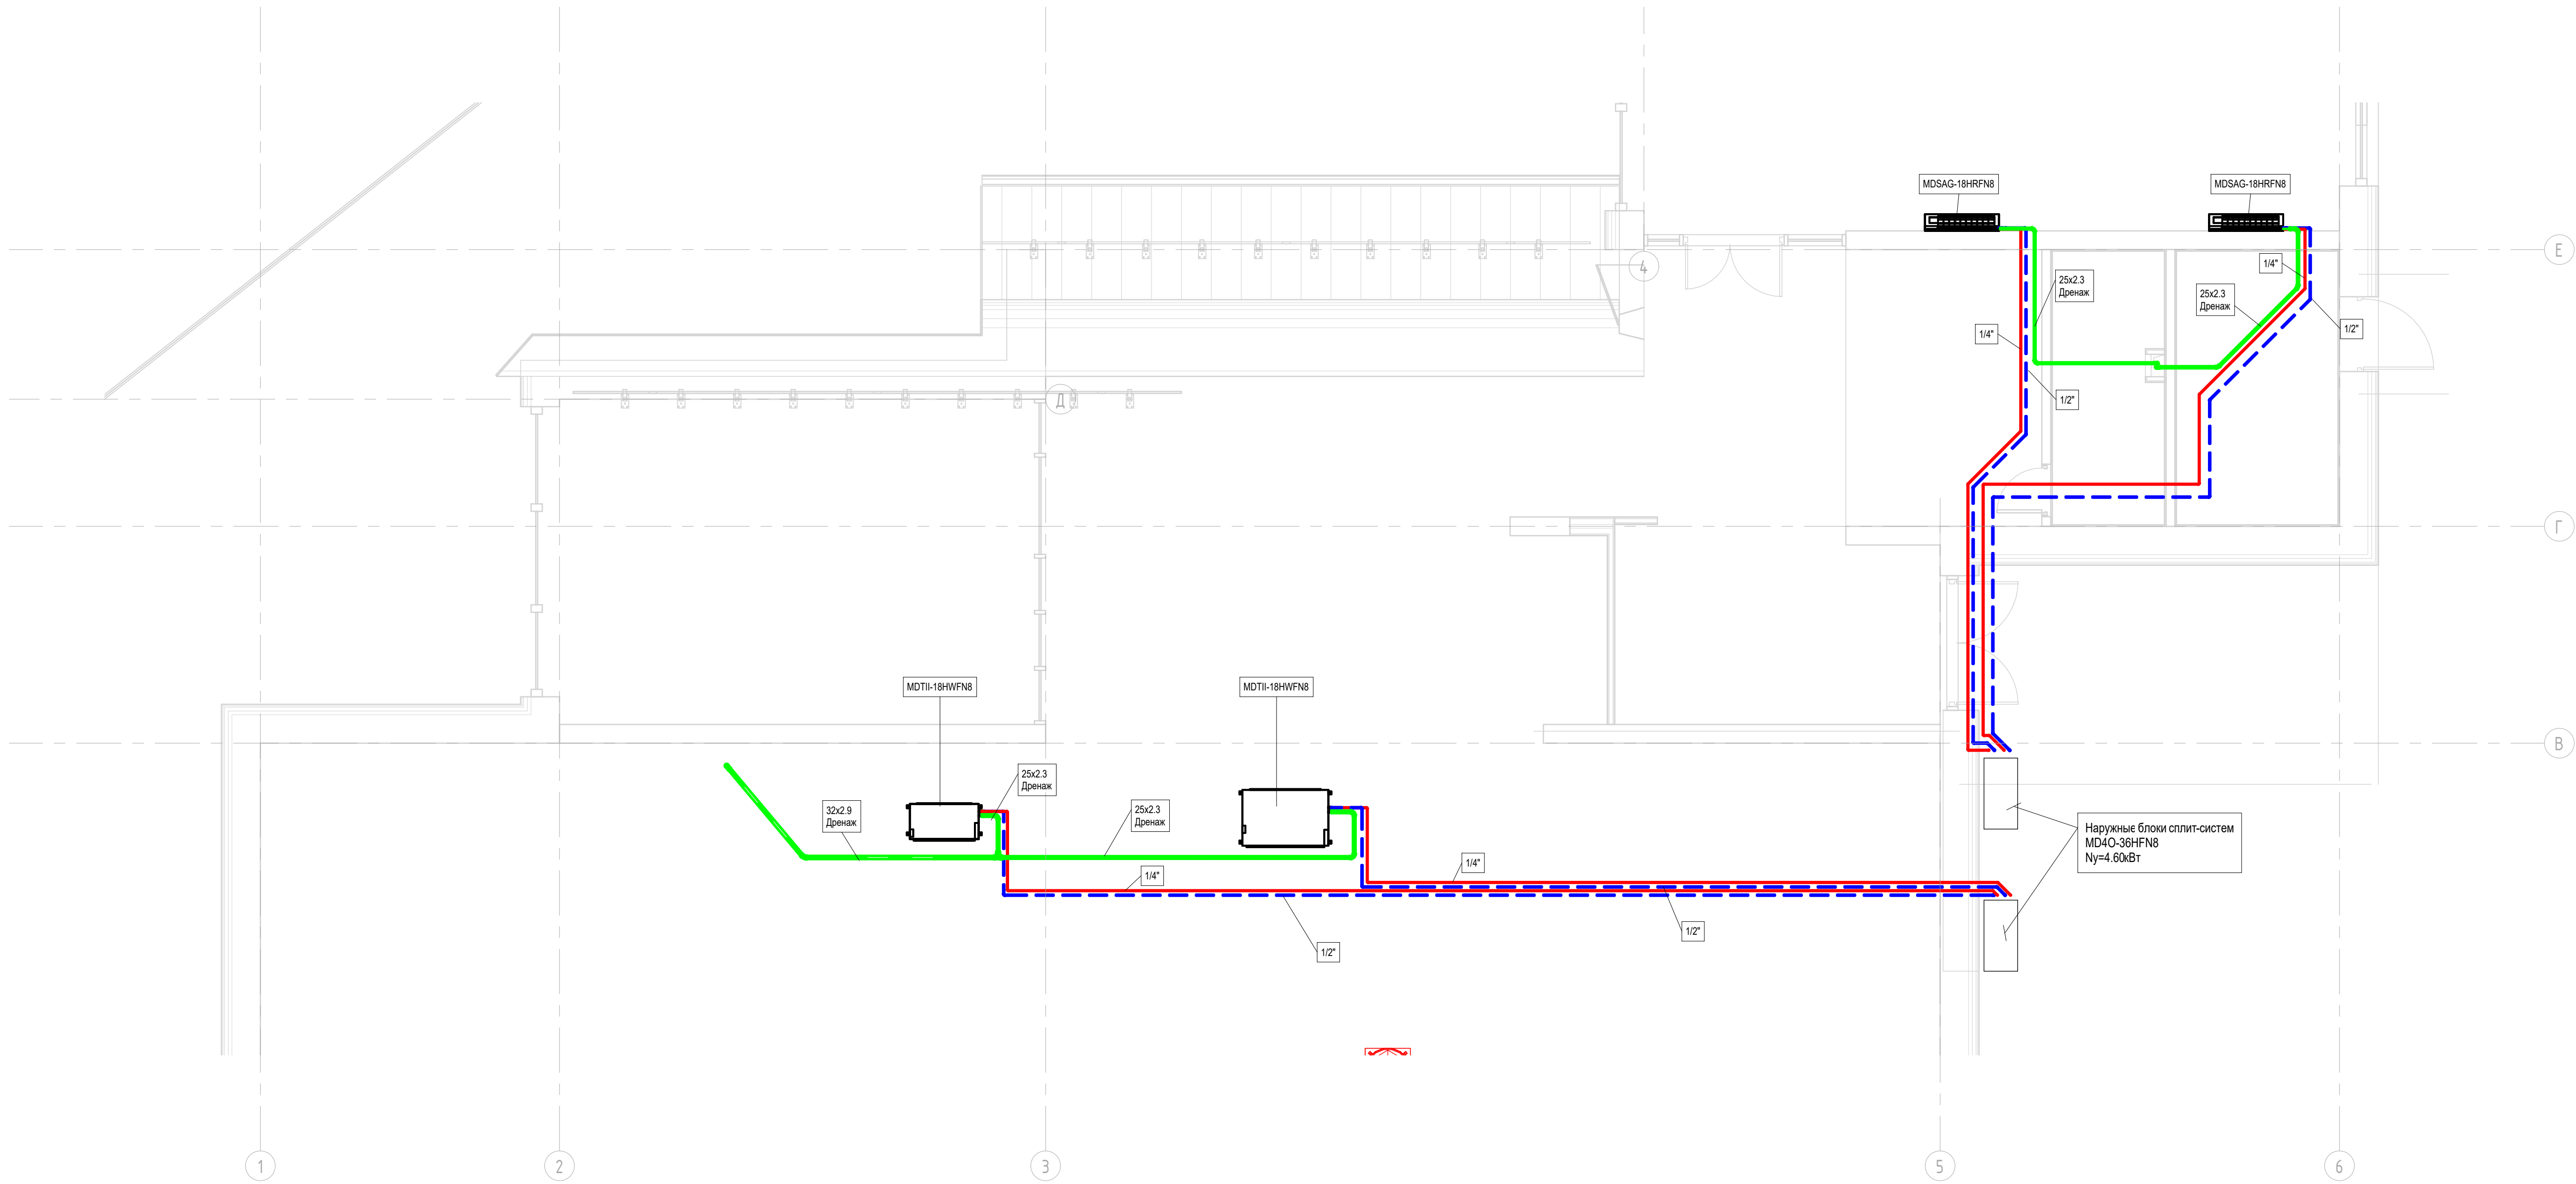

						ОВ2			
						Многофункциональный туристический центр "Николайские водопады"			
Изм.	Коп.уч.	Лист	№ док.	Подп.	Дата	Здание №04	Стадия	Лист	Листов
							Р	05	
						Палн на отм.+3.600. Кондиционирование			

Позиция	Наименование и техническая характеристика	Тип, марка, обозначение документа, опросного листа	Код оборудования, изделия, материала	Завод- изготовитель	Единица измерения	Количество	Масса ед. кг	Примечания					
1	2	3	4	5	6	7	8	9					
	Отопление												
1.	Конвектор внутривольный с естественной конвекцией, в комплекте с присоединительной грнитурой	SPL-NC-11/20-1700		SPL	шт.	6							
2.	Конвектор внутривольный с естественной конвекцией, в комплекте с присоединительной грнитурой	SPL-NC-11/30-1200		SPL	шт.	2							
3.	Конвектор внутривольный с естественной конвекцией, в комплекте с присоединительной грнитурой	SPL-NC-11/30-1900		SPL	шт.	2							
4.	Конвектор внутривольный с естественной конвекцией, в комплекте с присоединительной грнитурой	SPL-NC-11/30-3000		SPL	шт.	3							
5.	Стальной панельный радиатор с гладкой поверхностью с нижним подключением, вентильной вставкой, настенный, в комплекте присоединительной гарнитурой	SPL-CV(H)-10-500-800		SPL	шт.	4							
6.	Стальной панельный радиатор с гладкой поверхностью с нижним подключением, вентильной вставкой, настенный, в комплекте присоединительной гарнитурой	SPL-CV(H)-20-500-600		SPL	шт.	3							
7.	Стальной панельный радиатор с гладкой поверхностью с нижним подключением, вентильной вставкой, настенный, в комплекте присоединительной гарнитурой	SPL-CV(H)-20-500-800		SPL	шт.	4							
8.	Стальной панельный радиатор с гладкой поверхностью с нижним подключением, вентильной вставкой, настенный, в комплекте присоединительной гарнитурой	SPL-CV(H)-20-500-900		SPL	шт.	3							
9.	Стальной панельный радиатор с гладкой поверхностью с нижним подключением, вентильной вставкой, настенный, в комплекте присоединительной гарнитурой	SPL-CV(H)-20-500-1400		SPL	шт.	3							
10.	Коллекторная группа	SPL-DCU-BV-CS50-5R-20-R20R-P20R-B15R		SPL	Компл.	1							
11.	Труба из сшитого полиэтилена 16x2.2			SPL	п.м.	360							
12.	Труба из сшитого полиэтилена 20x2.8			SPL	п.м.	90							
13.	Труба из сшитого полиэтилена 25x3.5			SPL	п.м.	100							
14.	Трубка теплоизолирующая Ф16, толщина 6мм	ПУ-Флекс		ПУ-Флекс	п.м.	370							
15.	Трубка теплоизолирующая Ф20, толщина 6мм	ПУ-Флекс		ПУ-Флекс	п.м.	110							
16.	Трубка теплоизолирующая Ф25, толщина 6мм	ПУ-Флекс		ПУ-Флекс	п.м.	120							
17.	Конвектор электрический	Enzo BEC/EZER-1000		Ballu	шт.	1							
	Вентиляция												
18.	Вентилятор крышный радиальный	КРОВ60-035-T200-Н-00220/2-У1		BE3A	шт.	7							
19.	Вентилятор крышный радиальный, взрывозащищенный	КРОВ60-035-T200-		BE3A	шт.	1							
							ОВ2-СО						
			Изм.	Кол.	Лист	№д	Подпись	Дата					
			Разработал		Слюзов				Отопление, вентиляция и кондиционирование воздуха		Стадия	Лист	Листов
											Р	1	4
			Н. контроль						Спецификация оборудования, изделий и материалов.				
Инв. №		Дог.№											

1		2	3	4	5	6	7	8	9
одл.Инв. №Подпись и датаВзам. инв.			В-00220/2-У1						
		20. Вентилятор канальный	Канал-Вент-ЕС-160		ВЕЗА	шт.	3		
		21. Вентилятор канальный	Канал-КВАРК-В-56-56-2-400		ВЕЗА	шт.	4		
		22. Нагреватель канальный	Канал-КВН-80-50-3		ВЕЗА	шт.	4		
		23. Стакан монтажный для наклонных кровель	СТАМ-212-35-Н		ВЕЗА	шт.	8		
		24. Фильтр-бокс для прямоугольных каналов, в комплекте с фильтрующей вставкой F5	ФКПС 1000-700		ГалВент	шт.	4		
		25. Шумоглушитель пластинчатый прямоугольный, L=1500мм	ШПГ-1000x700-100/100-1500		ГалВент	шт.	4		
		26. Шумоглушитель пластинчатый прямоугольный, L=1000мм	ШПГ-1000x500-100/100-1000		ГалВент	шт.	4		
		27. Воздушный клапан ВК (Ar) 400x250	ABK		ГалВент	шт.	1		
		28. Воздушный клапан ВК (Ar) 600x250	ABK		ГалВент	шт.	2		
		29. Воздушный клапан ВК (Ar) 800x200	ABK		ГалВент	шт.	4		
		30. Воздушный клапан ВК (Ar) 800x250	ABK		ГалВент	шт.	4		
		31. Воздушный клапан ВК (Ar) 1000x700	ABK		ГалВент	шт.	4		
		32. Дроссель-клапан (Кр) Ø125	KBK		ГалВент	шт.	15		
		33. Дроссель-клапан (Кр) Ø160	KBK		ГалВент	шт.	2		
		34. Фильтр-искрогаситель, вертикальный	ГФ-3000		Filtech	шт.	2		
		35. Решетка щелевая скрытая с адаптером на 3 подключения Ø160, 1000x260	Эир Профи		Scheberg	шт.	2		
		36. Решетка щелевая скрытая с адаптером на 6 подключения Ø160, 2000x260	Эир Профи		Scheberg	шт.	3		
		37. Диффузор вытяжной круглого сечения	Ø125		ГалВент	шт.	15		
		38. Диффузор вытяжной круглого сечения	Ø160		ГалВент	шт.	2		
		39. Зонт круглого сечения	Ø160		ГалВент	шт.	3		
		40. Решетка ГАЛ-Н заборная наружная	1000x700		ГалВент	шт.	4		
		41. Решетка однорядная ГАЛ-1Р вытяжная	400x400		ГалВент	шт.	1		
		42. Решетка однорядная ГАЛ-1Р приточная	800x200		ГалВент	шт.	21		
		43. Воздуховод прямоугольный	300x400			п.м.	8		
		44. Воздуховод прямоугольный	400x200			п.м.	7		
		45. Воздуховод прямоугольный	400x250			п.м.	2		
		46. Воздуховод прямоугольный	400x400			п.м.	22		
		47. Воздуховод прямоугольный	600x250			п.м.	10		
		48. Воздуховод прямоугольный	800x200			п.м.	13		
		49. Воздуховод прямоугольный	800x250			п.м.	23		
		50. Воздуховод прямоугольный	800x500			п.м.	26		
		51. Воздуховод прямоугольный	850x550			п.м.	1		
		52. Воздуховод прямоугольный	1000x500			п.м.	1		
		53. Воздуховод прямоугольный	1000x700			п.м.	4		
		54. Воздуховод круглый	Ø125			п.м.	28		
		55. Воздуховод круглый	Ø160			п.м.	28		
		56. Воздуховод круглый	Ø315			п.м.	10		
		57. Воздуховод круглый	Ø355			п.м.	5		
		58. Врезка круглого сечения в круглый воздуховод	Ø125-Ø125			шт.	12		
		59. Врезка круглого сечения в круглый воздуховод	Ø160-Ø160			шт.	24		
		60. Врезка круглого сечения в круглый воздуховод	Ø315-Ø315			шт.	6		

1		2		3		4		5		6		7		8		9	
61.	Врезка круглого сечения в круглый воздуховод			ø355-ø355						шт.		2					
62.	Врезка прямоугольного сечения в круглый воздуховод			400x400-400x400						шт.		2					
63.	Врезка прямоугольного сечения в круглый воздуховод			800x250-800x250						шт.		1					
64.	Врезка прямоугольного сечения в плоскость			400x400-400x400						шт.		2					
65.	Врезка прямоугольного сечения в плоскость			600x250-600x250						шт.		1					
66.	Врезка прямоугольного сечения в плоскость			734x147-734x147						шт.		2					
67.	Врезка прямоугольного сечения в плоскость			800x200-800x200						шт.		21					
68.	Врезка прямоугольного сечения в плоскость			952x147-952x147						шт.		2					
69.	Заглушка прямоугольного сечения			300x400						шт.		4					
70.	Заглушка прямоугольного сечения			400x200						шт.		4					
71.	Заглушка прямоугольного сечения			400x250						шт.		1					
72.	Заглушка прямоугольного сечения			400x400						шт.		5					
73.	Заглушка прямоугольного сечения			600x250						шт.		2					
74.	Заглушка прямоугольного сечения			800x250						шт.		4					
75.	Отвод круглого сечения штампованный			ø125-ø125						шт.		19					
76.	Отвод круглого сечения штампованный			ø160-ø160						шт.		16					
77.	Отвод круглого сечения штампованный			ø315-ø315						шт.		3					
78.	Отвод круглого сечения штампованный			ø355-ø355						шт.		6					
79.	Отвод прямоугольного сечения			200x800-200x800						шт.		4					
80.	Отвод прямоугольного сечения			300x400-300x400						шт.		4					
81.	Отвод прямоугольного сечения			400x200-400x200						шт.		2					
82.	Отвод прямоугольного сечения			400x400-400x400						шт.		4					
83.	Отвод прямоугольного сечения			600x250-600x250						шт.		1					
84.	Отвод прямоугольного сечения			800x250-800x250						шт.		2					
85.	Отвод прямоугольного сечения			800x500-800x500						шт.		7					
86.	Переход из прямоугольного сечения на круглое сечение			400x400-ø160						шт.		2					
87.	Переход из прямоугольного сечения на круглое сечение			400x400-ø400						шт.		2					
88.	Переход из прямоугольного сечения на круглое сечение			600x250-ø400						шт.		2					
89.	Переход круглого сечения			ø160-ø125						шт.		3					
90.	Переход с прямоугольного сечения на прямоугольное сечение			400x400-355x355						шт.		8					
91.	Переход с прямоугольного сечения на прямоугольное сечение			800x500-600x250						шт.		1					
92.	Переход с прямоугольного сечения на прямоугольное сечение			800x500-800x250						шт.		2					
93.	Переход с прямоугольного сечения на прямоугольное сечение			850x550-400x400						шт.		2					
94.	Переход с прямоугольного сечения на прямоугольное сечение			850x550-600x250						шт.		2					
95.	Переход с прямоугольного сечения на прямоугольное сечение			1000x500-560x560						шт.		4					
96.	Переход с прямоугольного сечения на прямоугольное сечение			1000x500-800x500						шт.		4					
97.	Переход с прямоугольного сечения на прямоугольное сечение			1000x700-560x560						шт.		4					
98.	Тройник прямоугольного сечения			800x500-800x500-400x250						шт.		1					
99.	Тройник прямоугольного сечения			800x500-800x500-800x250						шт.		1					
100.	Крепежные элементы									кг.		15				Уточняется при монтаже	
	Кондиционирование воздуха																
101.	Наружный блок мультисплит системы			MD4O-36HFN8				MDV		шт.		2					
102.	Внутренний блок мультисплит системы			MDSAG-18HRFN8				MDV		шт.		2					
103.	Внутренний блок мультисплит системы			MDTII-18HRFN8				MDV		шт.		2					
104.	Труба медная 1/4"									п.м.		60					
105.	Труба медная 1/2"									п.м.		60					

1		2		3		4		5		6		7		8		9																	
106.		Трубка теплоизолирующая ¼“, толщина 16мм		РУ-Флекс				РУ-Флекс		п.м.		65																					
107.		Трубка теплоизолирующая 1/2“, толщина 16мм		РУ-Флекс				РУ-Флекс		п.м.		65																					
108.		Труба полипропиленовая Ф25х2.3						Proaqua		п.м.		8																					
109.		Труба полипропиленовая Ф32х2.9						Proaqua		п.м.		9																					
Изм.																																	
Лист																																	
4																																	