

Инв. № подл.	Подп. и дата	Взаим. инв. №

ПОЯСНЕНИЯ К ПРОЕКТУ

Рабочие чертежи систем вентиляции и кондиционирования воздуха разработаны на основании:

- утвержденного технического задания;
- архитектурных чертежей;
- действующих нормативных документов:
 - СП 131.13130.2020 - "Строительная климатология";
 - СП 60.13130.2020 - "Отопление, вентиляция и кондиционирование воздуха";

Расчетные параметры наружного воздуха

Холодный период:

- температура -17°С.

Теплый период:

- температура +30°С (для систем вентиляции и кондиционирования воздуха);

Отопление

Теплоснабжение системы отопления осуществляется от отдельностоящей блочной котельной. Теплоноситель вода с параметрами 90/70°С.

Для гидравлической увязки с соседними зданиями пред распределительными коллекторами задания предусмотрена установка балансировочной арматуры. Трубопроводы системы отопления и сшитого полиэтилена (РЕ-Ха) с кислородозащитным слоем.

Разводка трубопроводов осуществляется в стяжке пола.

В качестве отопительных приборов в комнатах применены стальные панельные радиаторы с гладкой поверхностью и внутрипольные конвекторы. В ванных комнатах и санузлах применены дизайн-радиаторы из нержавеющей стали, данные радиаторы учтены в разделе АИ.

Вентиляция и кондиционирование воздуха

В здании предусмотрена механическая вытяжная вентиляция из санузлов и зоны кухни. В кухне предусмотрены вытяжные вентиляторы для подключения технологических вытяжных зонтов. Воздуховоды от зонтов теплоизолируются рулонными материалами из минеральной ваты.

Для предотвращения образования конденсата все воздуховоды теплоизолированы материалом из вспененного каучука.

Предусмотренные вытяжные вентиляторы санузлов и бытовых помещений допускают горизонтальный (потолок) и вертикальный (стена) мотнаж. Конкретный вариант мотнажа уточняется дизайн-проектом (см. раздел АИ)

ОБЩИЕ УКАЗАНИЯ

- Монтаж и сдачу в эксплуатацию систем вентиляции следует производить в соответствии с
 - СП 72.13130 "Внутренние санитарно-технические работы";

Все отступления от проектных решений должны быть согласованы с представителями авторского надзора.

- Привязки и отметки трубопроводов и воздуховодов уточнить при производстве монтажных замеров в натуре с учетом смонтированных строительных конструкций.

- Воздуховоды и детали вентиляционных систем должны быть изготовлены в соответствии с рабочей документацией и утверждены в установленном порядке техническими условиями.

- Присоединение воздуховодов к технологическому оборудованию должно производиться после его установки.

- Регулирующие приспособления (шибер, дроссель-клапаны, заслонки, регулирующие органы воздухораспределителей) должны легко закрываться и открываться, а также фиксироваться в заданном положении.

- Прокладку фреоновых трубопроводов через стены и перекрытия производить в гильзах. В местах пересечения стен и перекрытий трубопроводами образовавшиеся отверстия и зазоры заделать термоизолирующим материалами на всю глубину ограждения.

- Фреоновые трубопроводы прокладывать в изоляции. Изоляция должна плотно прилегать к поверхности трубопровода. Стыки тщательно проклеить и защитить армированной самоклеющейся лентой.

- Трубопроводы систем теплоснабжения, отопления и холодоснабжения должны быть испытаны гидростатическим или манометрическим методом с соблюдением требований СП 72.13130 и сданы по акту представителям технического надзора до производства теплоизоляционных работ. До испытания и теплоизоляции трубопроводов выполнить врезки и закладные детали устройств для приборов КИП и автоматики.

- Производство работ по монтажу оборудования производить, согласно требованиям производителя..

- Все проходы через противопожарные стены и перегородки должны быть заделаны сертифицированным герметиком. Места расположения противопожарных стен и перегородок смотреть на архитектурных чертежах.

- Все оборудование и материалы должны иметь соответствующие сертификаты РФ.

Ведомость рабочих чертежей основного комплекта ОВ4

Лист	Наименование	Примечание
01	Общие данные	-
02	План на отм.+0.000. Отопление	-
03	План на отм.+0.000. Кондиционирование воздуха	-
04	План на отм.+0.000. Вентиляция	-
05	Схема системы отпoления	-

Ведомость ссылочных и прилагаемых документов

Обозначение	Наименование	Примечание
ОВ5.1-СО	Спецификация оборудования, изделий и материалов	-


Ведомость основных комплектов марки ОВ

Обозначение	Наименование	Примечание
ОВ1	Здание №02	-
ОВ2	Здание №04	
ОВ3	Здание №01	
ОВ4	Здание №05	
ОВ5.1	Здание №06	
ОВ5.2	Здание №07	

Основные показатели по рабочим чертежам комплекта ОВ4

Наименование здания (сооружения), помещения	Объем, м3	Периоды года при tн, °С	Расход теплоты, Вт				Расход холода, Вт	Установленная мощность электродвигателей, кВт
			на отопление	на вентиляцию	на горячее водоснабжение	общий		
Здание №05	-	-17	7060	-	см. проект ВК	7060	-	2.12
	-	+30	-	-	см. проект ВК	-	7800	


						ОВ4			
Изм.	Кол.уч	Лист	№докум.	Подпись	Дата	Многофункциональный туристический центр "Нихалойские водопады"			
ГИП						Здание № 05	Стадия	Лист	Листов
Разработал		Слюзов					Р	01	
Норм.контр.						Общие данные			
Инв.№				Дог.№					

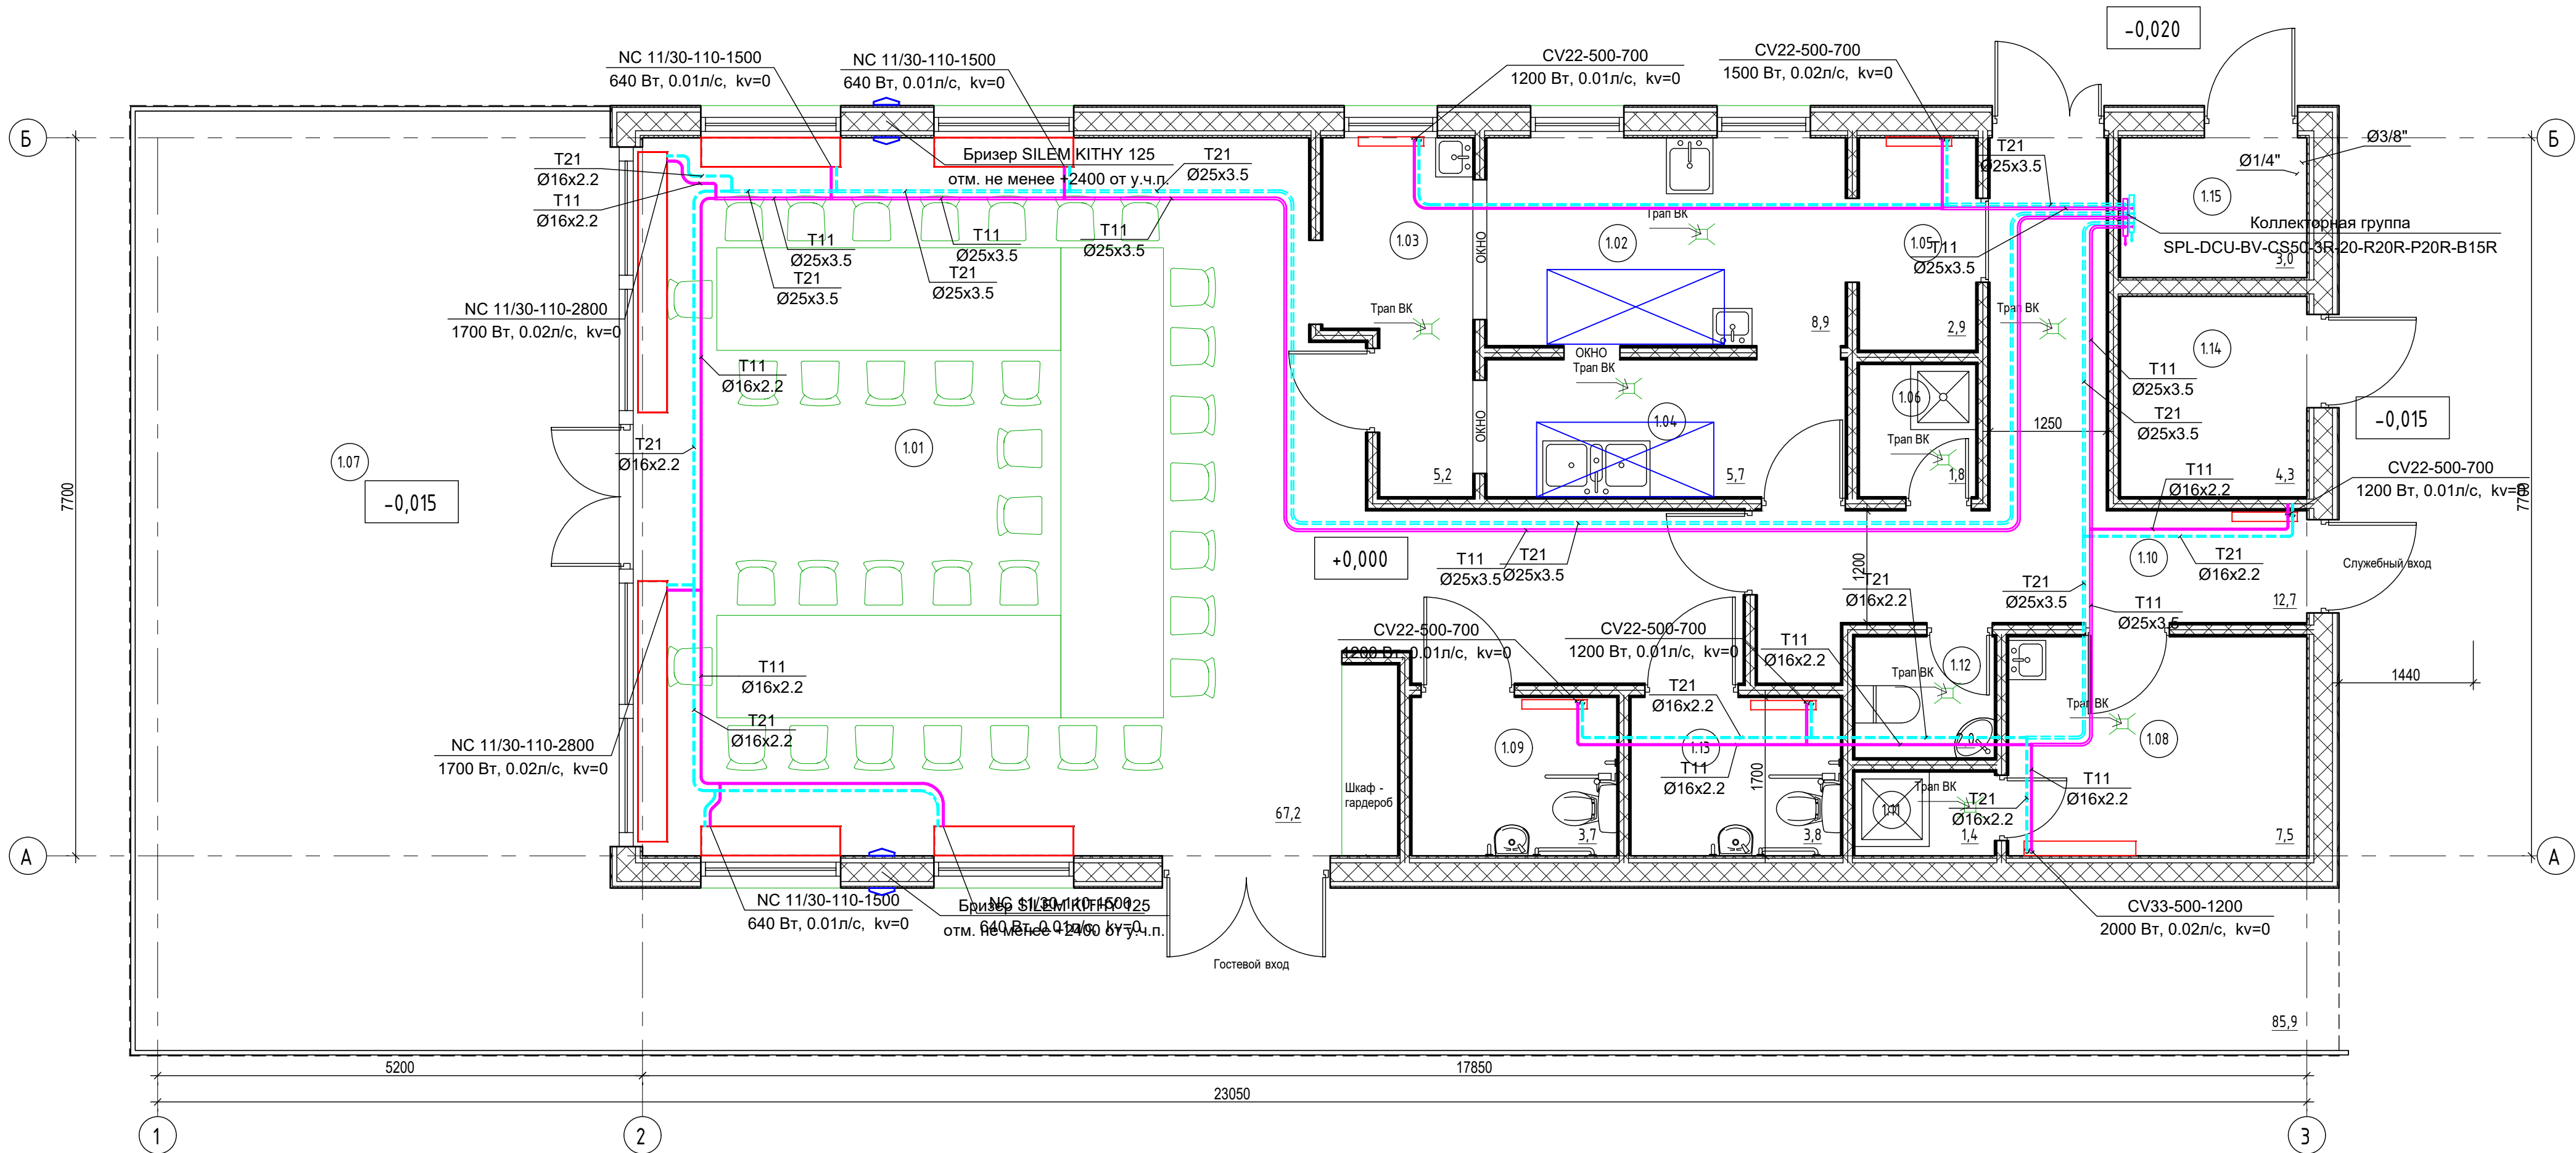

Экспликация помещений




Номер	Имя	Площадь, м2	Кат. пом.
1.01	Основной зал	67,2	
1.02	Доготовочная	8,9	
1.03	Раздаточная	5,2	
1.04	Моечная посуды	5,7	
1.05	Зона хранения	2,9	
1.06	ПУИ	1,8	
1.08	Раздевалка	7,5	
1.09	С/У М/ МГН	3,7	
1.10	Коридор	12,7	
1.11	Душевая	1,4	
1.12	С/У	2	
1.13	С/У Ж/ МГН	3,8	
1.14	Пом. ЗОМ	4,3	
1.15	Пом. ввода ВК	3	

						ОВ4			
Изм.	Кол.уч	Лист	Недок.	Подпись	Дата	Многофункциональный туристический центр "Нихалойские водопады"			
ГИП						Здание № 05	Стадия	Лист	Листов
Разработал	Слюзов						Р	02	
Норм.контр.						План на отм.+0.000. Отопление			
Инв.№				Дог.№					

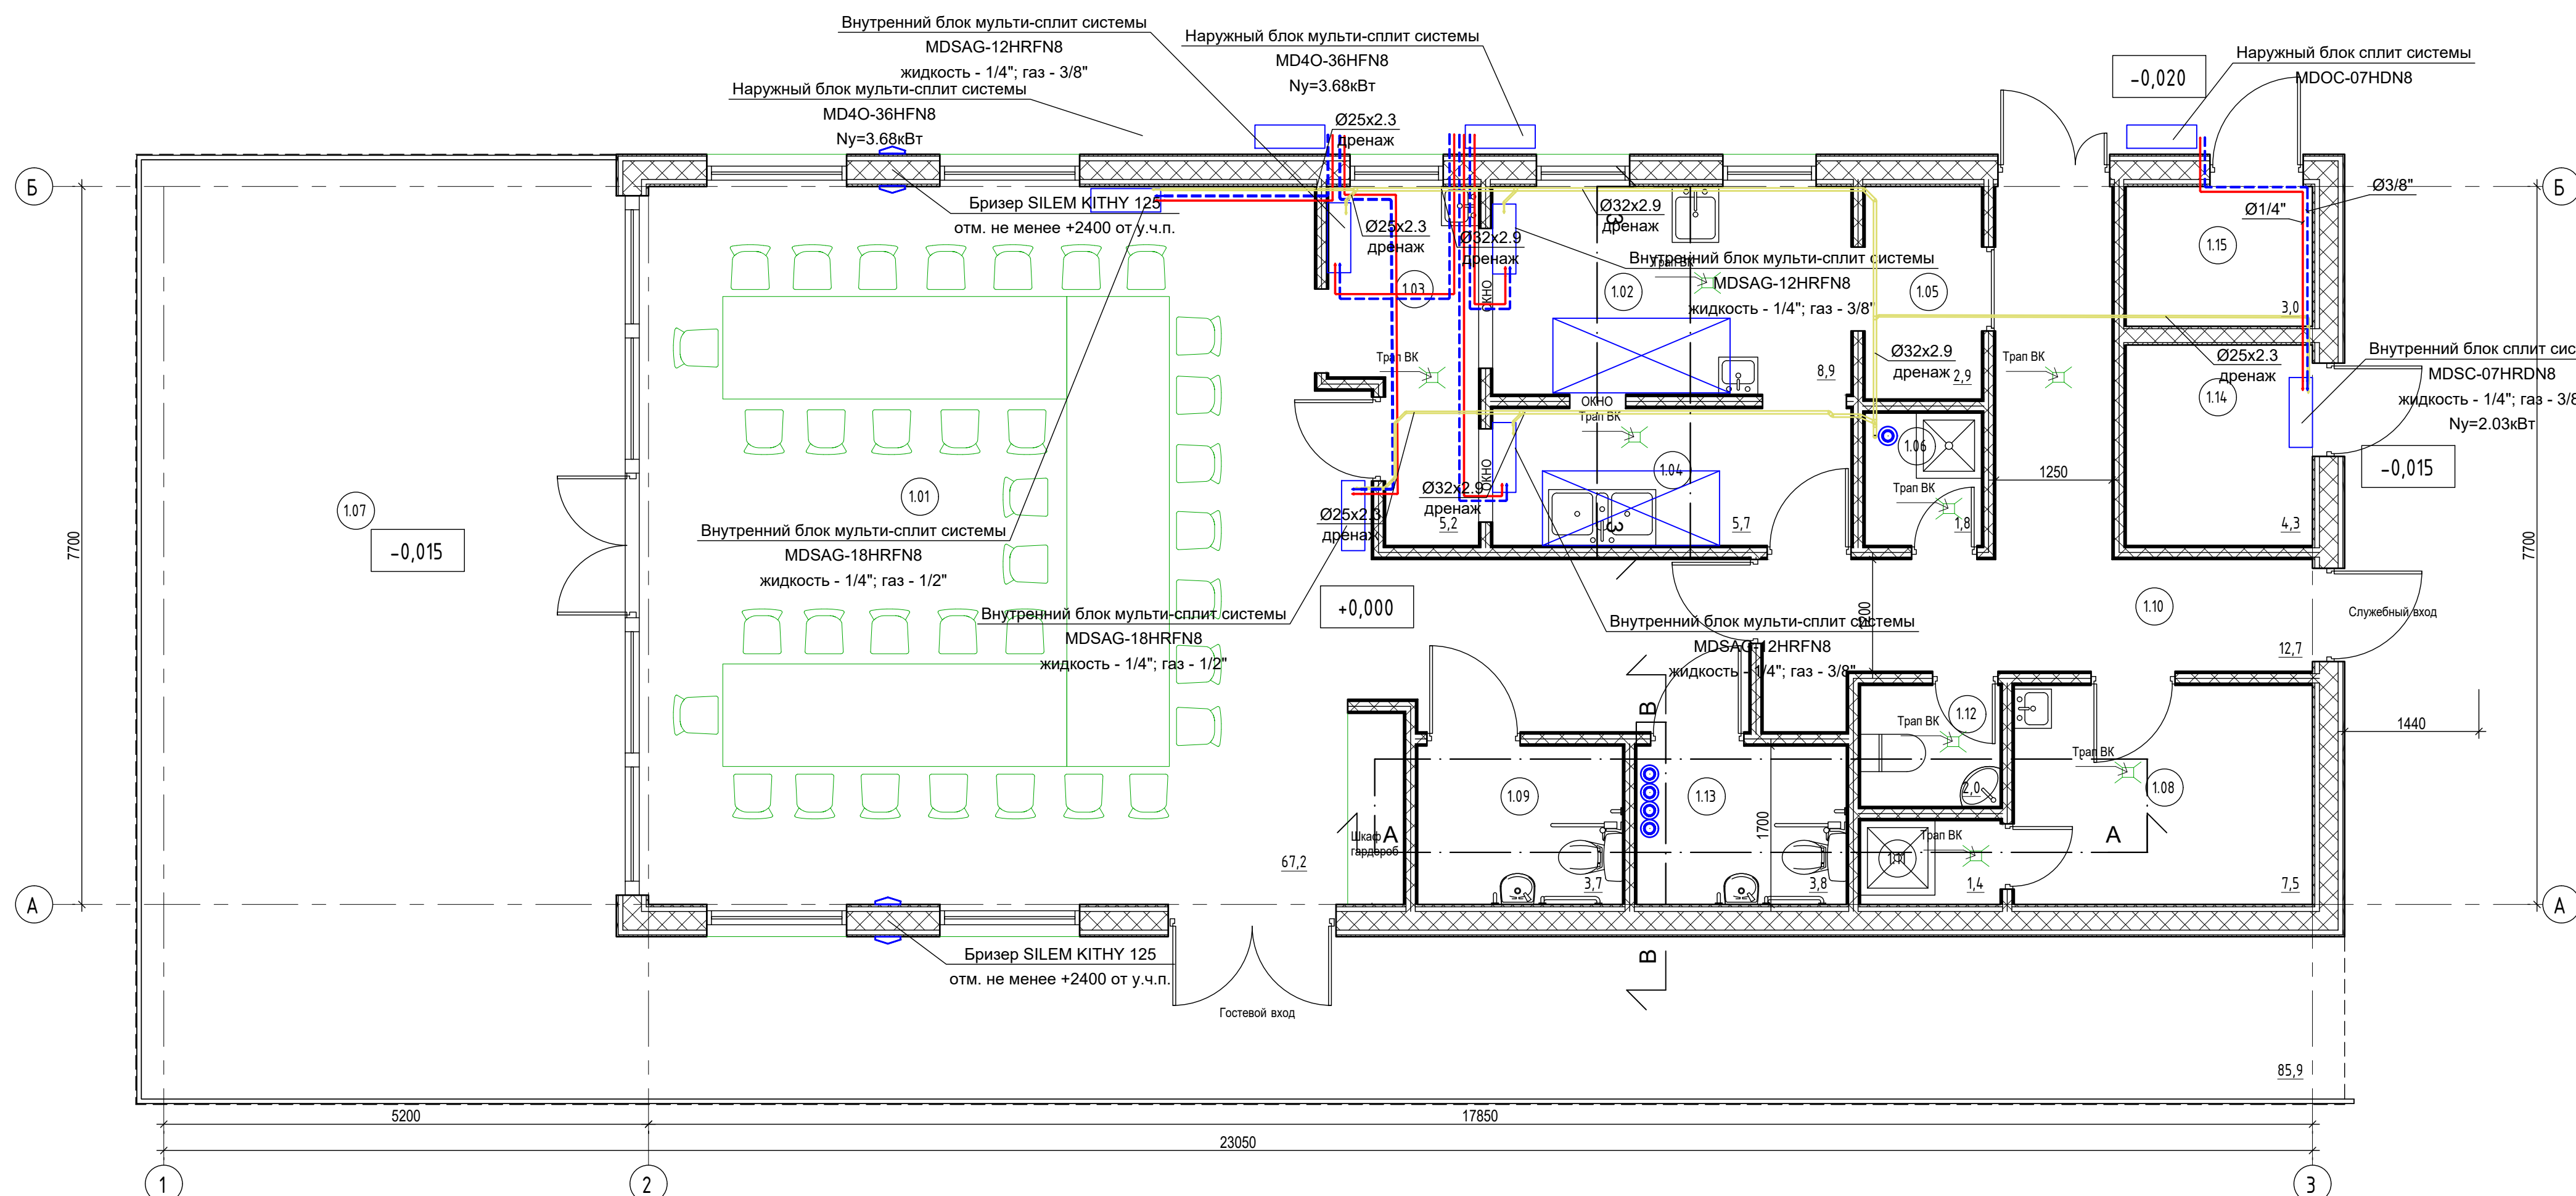

Экспликация помещений			
Номер	Имя	Площадь, м2	Кат. пом.
1.01	Основной зал	67,2	
1.02	Догоготовочная	8,9	
1.03	Раздаточная	5,2	
1.04	Моечная посуды	5,7	
1.05	Зона хранения	2,9	
1.06	ПУИ	1,8	
1.08	Раздевалка	7,5	
1.09	С/У М/ МГН	3,7	
1.10	Коридор	12,7	
1.11	Душевая	1,4	
1.12	С/У	2	
1.13	С/У Ж/ МГН	3,8	
1.14	Пом. ЭОМ	4,3	
1.15	Пом. ввода ВК	3	

						ОВ4			
Изм.	Кол.уч.	Лист	Недок.	Подпись	Дата	Многофункциональный туристический центр "Нихалойские водопады"			
ГИП						Здание № 05	Стадия	Лист	Листов
Разработал	Слюзов						Р	03	
Норм.контр.						план на отм.+0.000. Кондиционирование воздуха			
Инв.№				Дог.№					

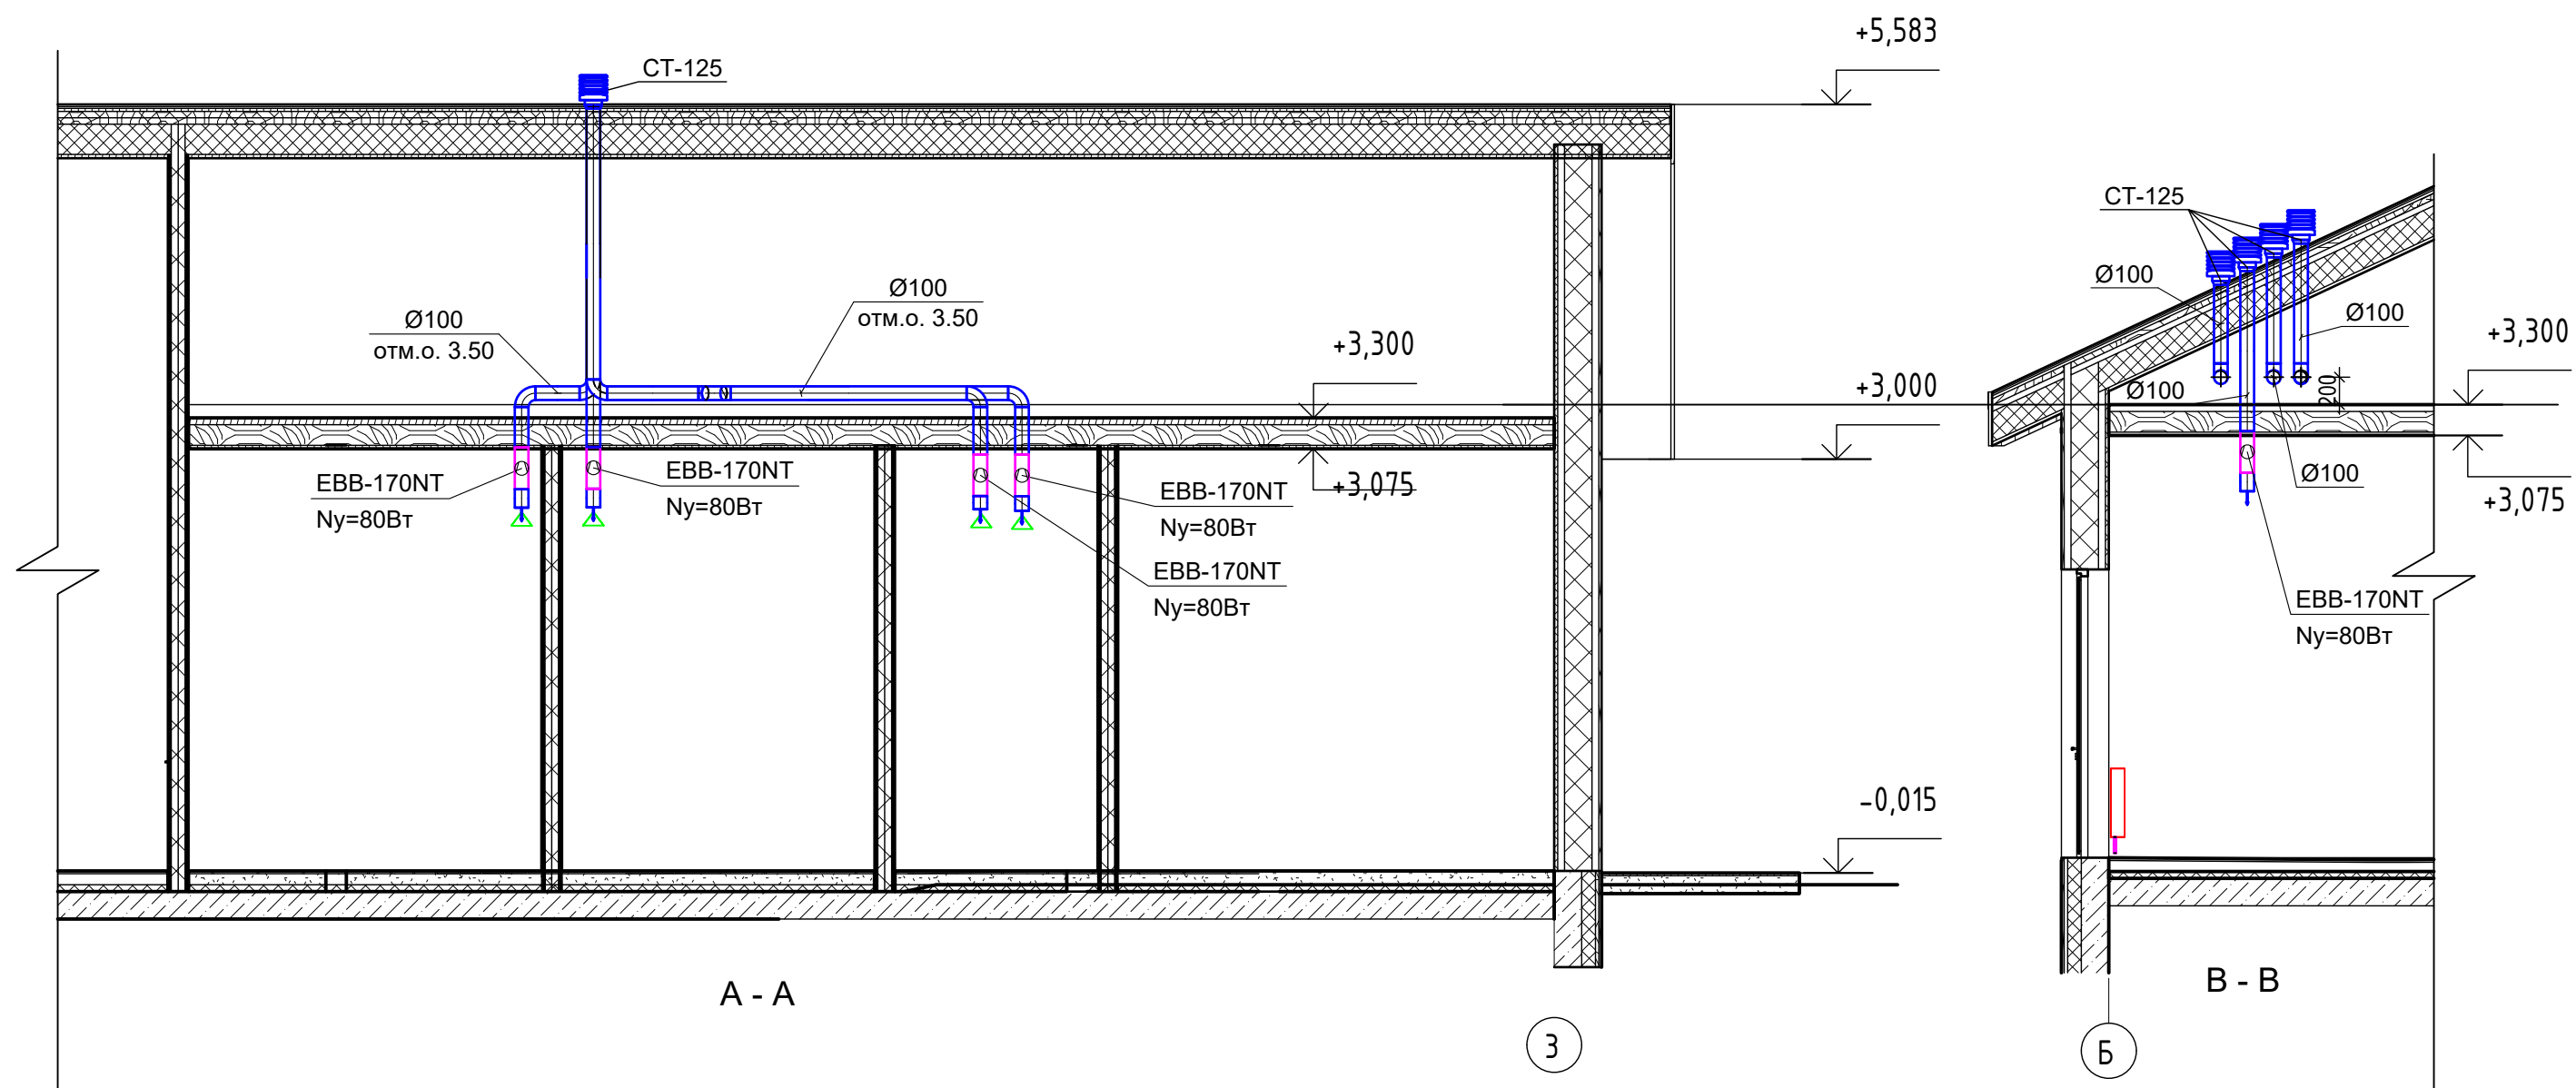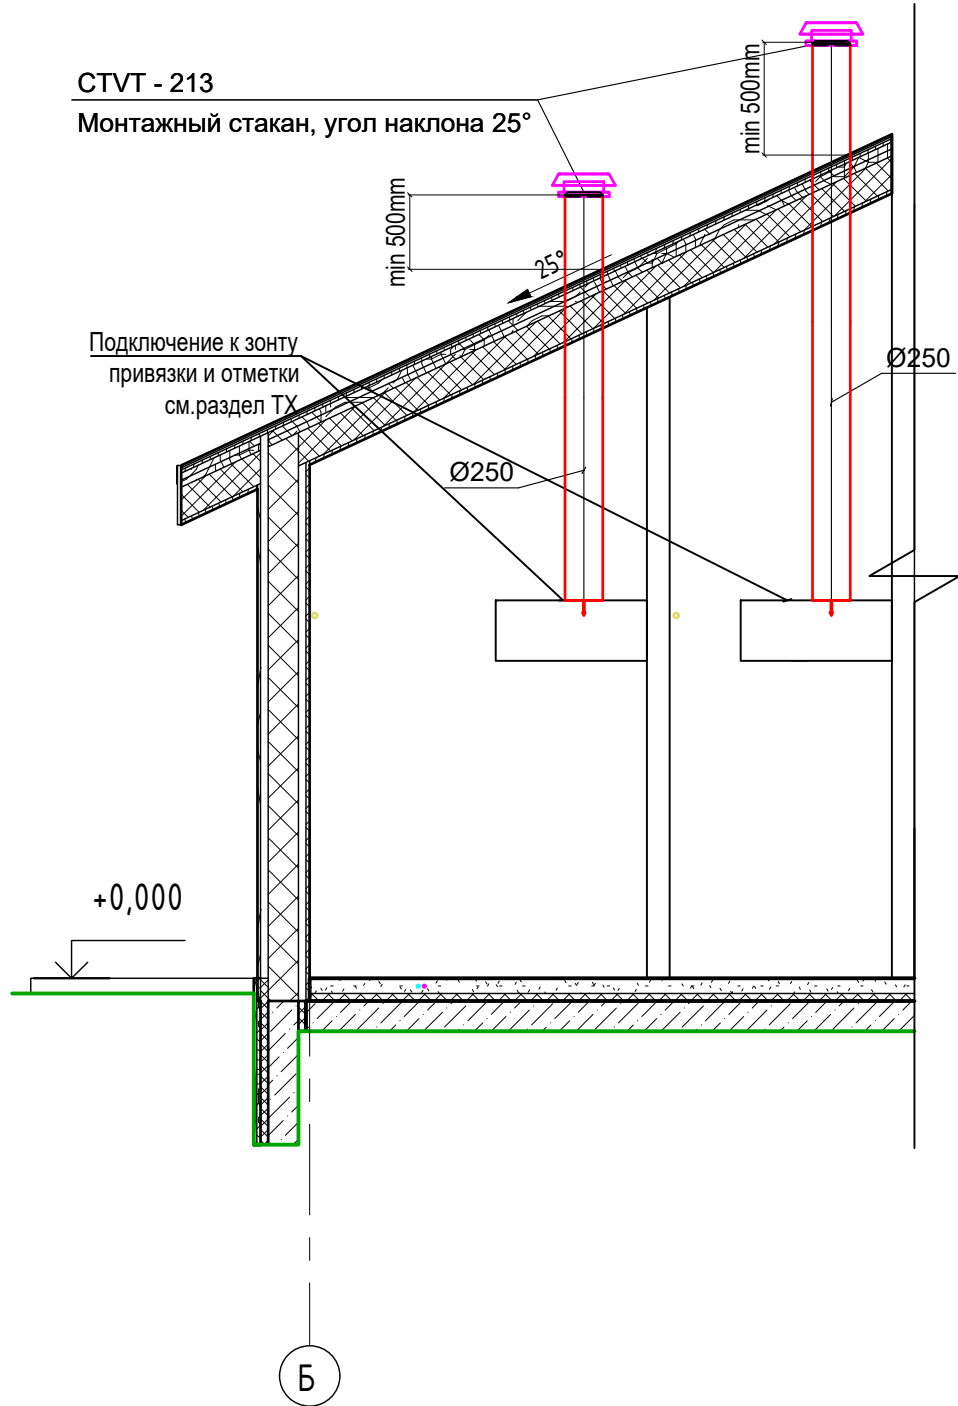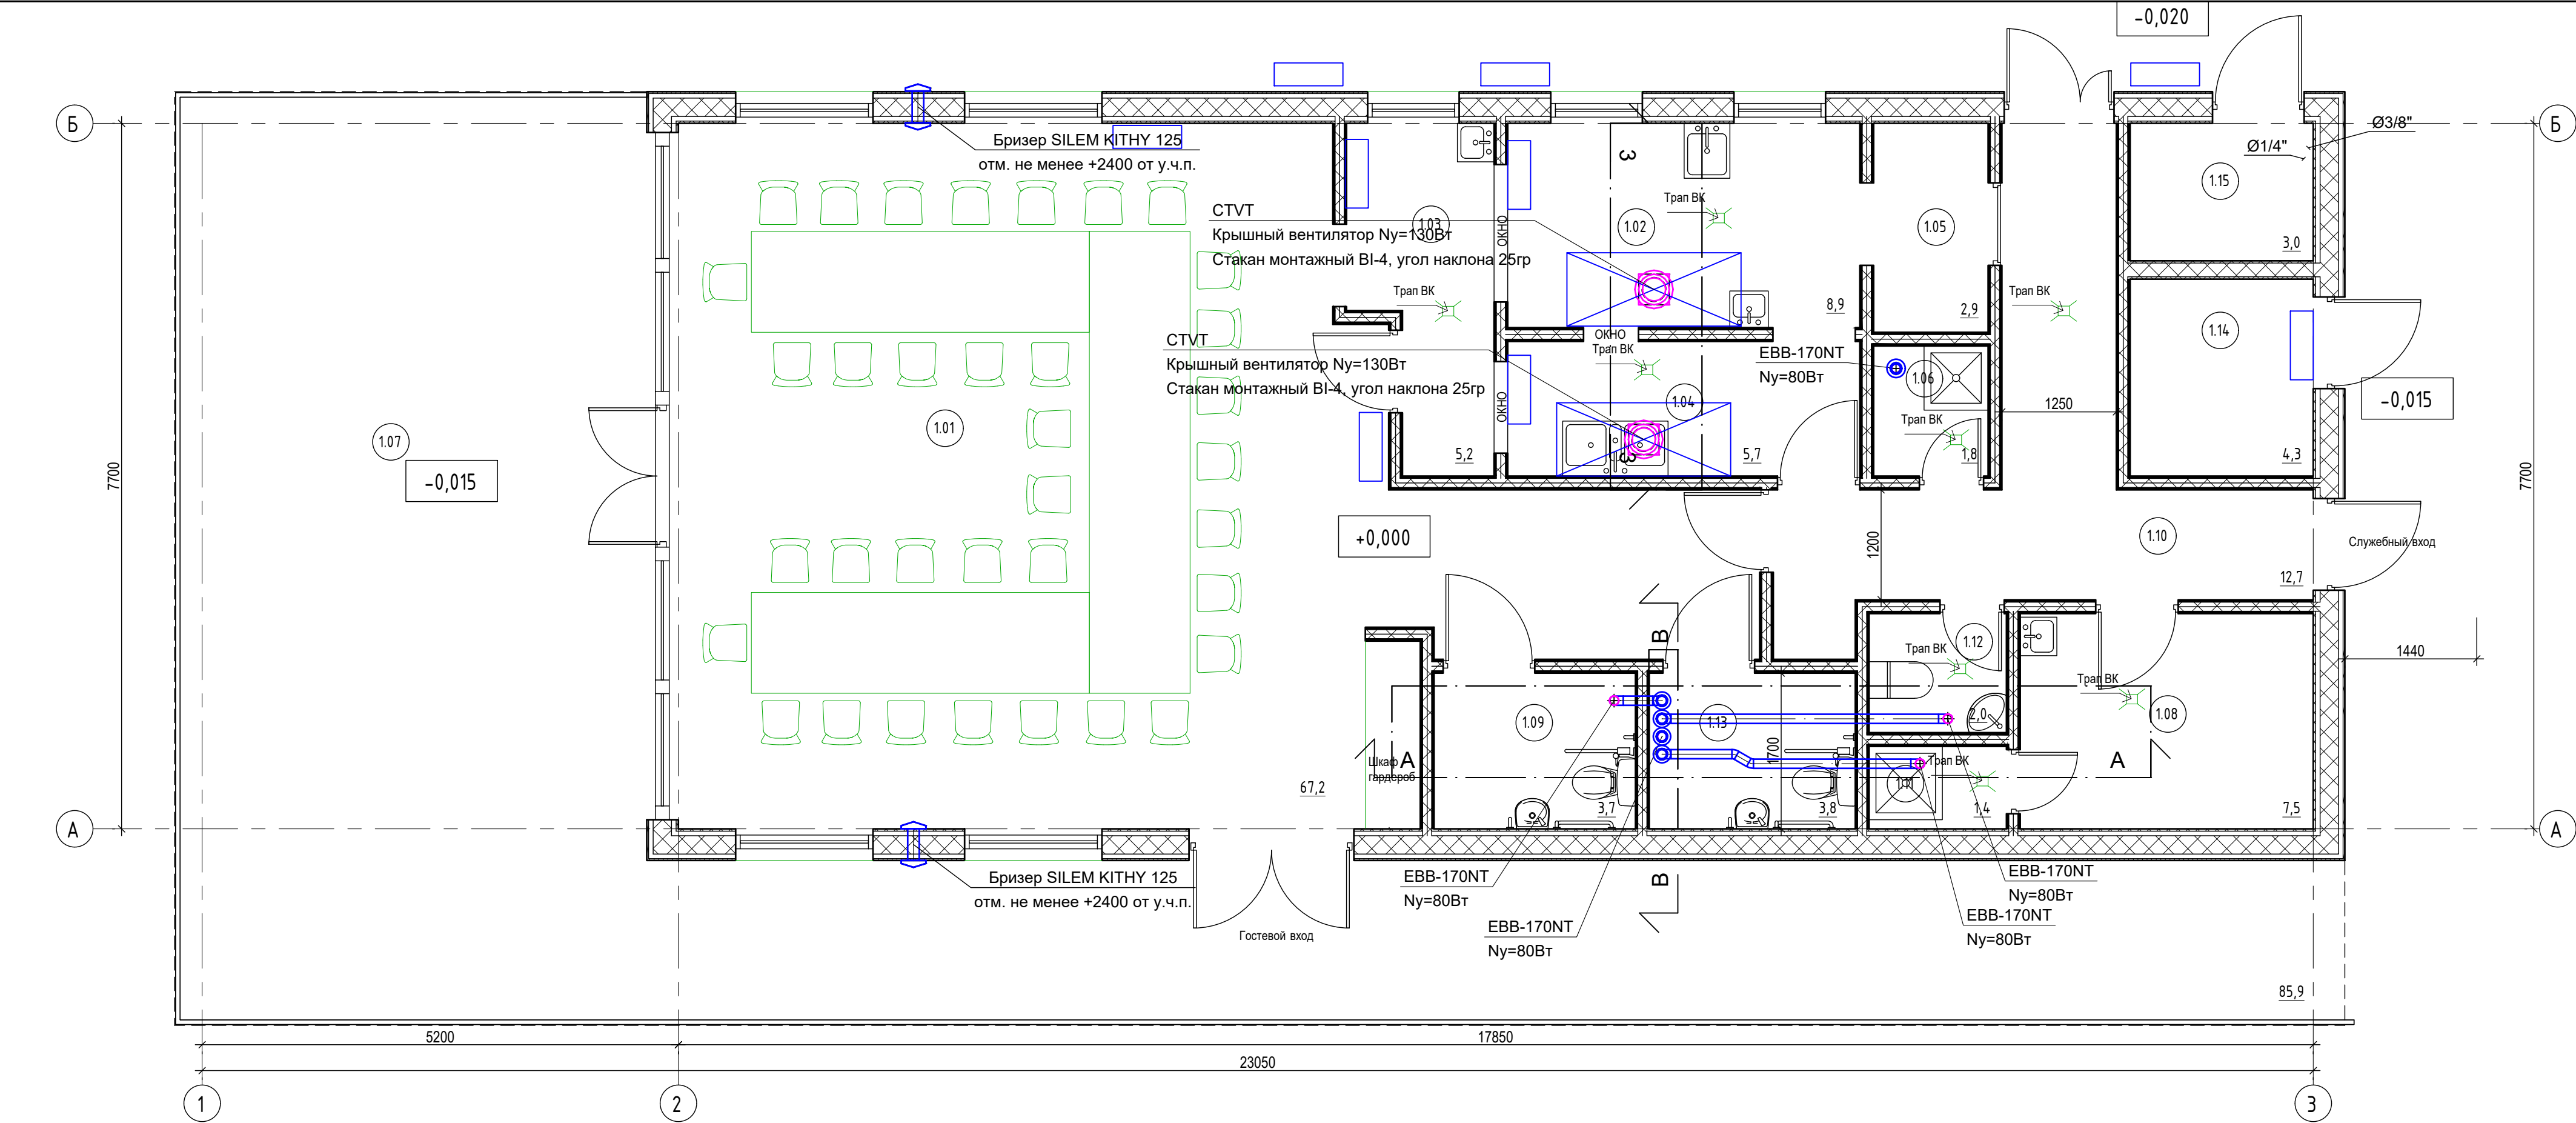

Экспликация помещений			
Номер	Имя	Площадь, м2	Кат. пом.
1.01	Основной зал	67,2	
1.02	Догоготовочная	8,9	
1.03	Раздаточная	5,2	
1.04	Моечная посуды	5,7	
1.05	Зона хранения	2,9	
1.06	ПУИ	1,8	
1.08	Раздевалка	7,5	
1.09	С/У М/ МГН	3,7	
1.10	Коридор	12,7	
1.11	Душевая	1,4	
1.12	С/У	2	
1.13	С/У Ж/ МГН	3,8	
1.14	Пом. ЭОМ	4,3	
1.15	Пом. ввода ВК	3	

						ОВ4		
Изм.	Кол.уч.	Лист	Недок.	Подпись	Дата	Многофункциональный туристический центр "Нихалойские водопады"		
ГИП						Здание № 05	Стадия	Лист
Разработал	Слюзов						Р	04
Норм.контр.						План на отм.+0.000. Вентиляция		
Инв.№				Дог.№				



Формат: А2

Позиция	Наименование и техническая характеристика	Тип, марка, обозначение документа, опросного листа	Код оборудования, изделия, материала	Завод- изготовитель	Единица измерения	Количество	Масса ед. кг	Примечания
1	2	3	4	5	6	7	8	9
	Отопление							
1.	Конвектор внутипольный с естественной конвекцией, в комплекте с присоединительной грнитурой	SPL-NC-11/30-1500		SPL	шт.	4		
2.	Конвектор внутипольный с естественной конвекцией, в комплекте с присоединительной грнитурой	SPL-NC-11/30-2800		SPL	шт.	2		
3.	Стальной панельный радиатор с нижним подключением, вентильной вставкой, настенный, в комплекте присоединительной гарнитурой	SPL-CC-22-500-700		SPL	шт.	5		
4.	Стальной панельный радиатор с нижним подключением, вентильной вставкой, настенный, в комплекте присоединительной гарнитурой	SPL-CC-33-500-1200		SPL	шт.	1		
5.	Коллекторная группа	SPL-DCU-BV-CS50-3R-20-R20R-P20R-B15R		SPL	Компл.	1		
6.	Труба из сшитого полиэтилена 16x2.2			SPL	п.м.	70		
7.	Труба из сшитого полиэтилена 25x3.5			SPL	п.м.	65		
8.	Тройник 16/16/16			SPL	шт.	6		
9.	Тройник 25/25/16			SPL	шт.	12		
10.	Соединитель 25/16			SPL	шт.	6		
11.	Пластиковый башмак 16			SPL	шт.	6		
12.	Трубка теплоизолирующая Ф16, толщина 6мм	ПУ-Флекс		ПУ-Флекс	п.м.	70		
13.	Трубка теплоизолирующая Ф25, толщина 6мм	ПУ-Флекс		ПУ-Флекс	п.м.	65		
	Вентиляция							
14.	Вентилятор крышный с вертикальным выбросом, высокотемпературный, L=500м3/ч, P=170Па	CTVT/4-200		Soler&palau	шт.	2		
15.	Обратный клапан	JCA-435		Soler&palau	шт.	2		
16.	Основание для наклонной кровли, угол кровли 25 градусов	BI-4, угол 25 гр.		Soler&palau	шт.	2		
17.	Вентилятор бытовой настенный со встроенным таймером	EBB-170NT		Soler&palau	шт.	5		
18.	Металлический крышный зонт	CT-125 TEJA		Soler&palau	шт.	5		
19.	Гигрорегулируемый приточный клапан	SILEM KIT HY 125		Soler&palau	шт.	2		
20.	Воздуховод из оцинкованной стали толщиной 0.5 мм	Ф100			п.м.	12		
21.	Воздуховод из оцинкованной стали толщиной 0.5 мм	Ф250			п.м.	4		
22.	Отвод 90гр. из оцинкованной стали толщиной 0.5 мм	Ф100			шт.	6		
23.	Отвод 30гр. из оцинкованной стали толщиной 0.5 мм	Ф100			шт.	2		
24.	Переход из оцинкованной стали толщиной 0.5 мм	Ф100/Ф125			шт.	5		
25.	Теплоизоляция из вспененого каучука	ПУ-Флекс		ПУ-Флекс	кв.м.	4		
26.	Крепежные элементы				кг.	15		Уточняется при

						ОВ4-СО				
Изм.	Кол.	Лист	№д	Подпись	Дата					
						Отопление, вентиляция и кондиционирование воздуха		Стадия	Лист	Листов
Разработал	Слюзов				Р			1	2	
						Спецификация оборудования, изделий и материалов.				
Н. контроль										
Инв. №				Дог.№						

1	2	3	4	5	6	7	8	9
								МОНТАЖЕ
	Кондиционирование воздуха							
27.	Наружный блок мультисплит системы	MD4O-36HFN8		MDV	шт.	2		
28.	Внутренний блок мультисплит системы	MDSAG-12HRFN8		MDV	шт.	3		
29.	Внутренний блок мультисплит системы	MDSAG-18HRFN8		MDV	шт.	2		
30.	Наружный блок сплит системы	MDOC-07HDN8		MDV	шт.	1		
31.	Внутренний блок сплит системы	MDSC-07HRDN8		MDV	шт.	1		
32.	Труба медная 1/4"				п.м.	37		
33.	Труба медная 3/8"				п.м.	27		
34.	Труба медная 1/2"				п.м.	20		
35.	Трубка теплоизолирующая 1/4", толщина 16мм	ПУ-Флекс		ПУ-Флекс	п.м.	30		
36.	Трубка теплоизолирующая 3/8", толщина 16мм	ПУ-Флекс		ПУ-Флекс	п.м.	20		
37.	Трубка теплоизолирующая 1/2", толщина 16мм	ПУ-Флекс		ПУ-Флекс	п.м.	20		
38.	Труба полипропиленовая Ф25х2.3			Proaqua	п.м.	12		
39.	Труба полипропиленовая Ф32х2.9			Proaqua	п.м.	10		

					ОВ4-СО	Лист
						2
Изм.	Лист	№ лок.	Подп.	Дата		