

Спортивно-туристический комплекс
«Нихалоевские Водопады»
по адресу: Чеченская Республика, р-н Шатойский,
с. Нихалой, в границах земельного участка
с кадастровым номером 20:14:4102000:118

РАБОЧАЯ ДОКУМЕНТАЦИЯ

Отопление. Вентиляция. Кондиционирование.

Гостевой дом поз. №6 по ГП

01-00-ОВ5.1

Согласовано		
Взамен инв. №		
Подп. и дата		
Инв. № подл.		

Изм.	№ док.	Подпись	Дата

2025 г.

Инв. № подл.	Подп. и дата	Взаим. инв. №

ПОЯСНЕНИЯ К ПРОЕКТУ

Рабочие чертежи систем вентиляции и кондиционирования воздуха разработаны на основании:

- утвержденного технического задания;
- архитектурных чертежей;
- действующих нормативных документов:
 - СП 131.13130.2020 - "Строительная климатология";
 - СП 60.13130.2020 - "Отопление, вентиляция и кондиционирование воздуха";

Расчетные параметры наружного воздуха

Холодный период:

- температура -17°С.

Теплый период:

- температура +30°С (для систем вентиляции и кондиционирования воздуха);

Отопление

Теплоснабжение системы отопления осуществляется от отдельностоящей блочной котельной. Теплоноситель вода с параметрами 90/70°С.

Для гидравлической увязки с соседними зданиями пред распределительными коллекторами задания предусмотрена установка балансировочной арматуры. Трубопроводы системы отопления и сшитого полиэтилена (РЕ-Ха) с кислородозащитным слоем.

Разводка трубопроводов осуществляется в стяжке пола.

В качестве отопительных приборов в комнатах применены внутрипольные конвекторы с естественной конвекцией. В ванных комнатах и санузлах применены дизайн-радиаторы из нержавеющей стали, данные радиаторы учтены в разделе АИ.

Вентиляция и кондиционирование воздуха

В здании предусмотрена механическая вытяжная вентиляция из санузлов и зоны кухни. В кухне предусмотрен отдельный вытяжной канал для подключения вытяжного зонта от плиты. Обратный клапан должен быть предусмотрен в составе зонта. До подключения зонта вытяжной канал заглушить.

Для предоптващения образования конденсата все воздухопроводы теплоизолированы материалом из вспененного каучука.

Предусмотренные вытяжные вентиляторы допускают горизонтальный (потолок) и вертикальный (стена) мотнаж.

Конкретный вариант мотнажа уточняется дизайн-проектом (см. раздел АИ)

ОБЩИЕ УКАЗАНИЯ

1. Монтаж и сдачу в эксплуатацию систем вентиляции следует производить в соответствии с

- СП 72.13130 "Внутренние санитарно-технические работы";

Все отступления от проектных решений должны быть согласованы с представителями авторского надзора.

2. Привязки и отметки трубопроводов и воздухопроводов уточнить при производстве монтажных замеров в натуре с учетом смонтированных строительных конструкций.

3. Воздуховоды и детали вентиляционных систем должны быть изготовлены в соответствии с рабочей документацией и утверждены в установленном порядке техническими условиями.

4. Присоединение воздухопроводов к технологическому оборудованию должно производиться после его установки.

5. Регулирующие приспособления (шибер, дроссель-клапаны, заслонки, регулирующие органы воздухораспределителей) должны легко закрываться и открываться, а также фиксироваться в заданном положении.

6. Прокладку фреоновых трубопроводов через стены и перекрытия производить в гильзах. В местах пересечения стен и перекрытий трубопроводами образовавшиеся отверстия и зазоры заделать термоизолирующим материалами на всю глубину ограждения.

7. Фреоновые трубопроводы прокладывать в изоляции. Изоляция должна плотно прилегать к поверхности трубопровода. Стыки тщательно проклеить и защитить армированной самоклеющейся лентой.

8. Трубопроводы систем теплоснабжения, отопления и холодоснабжения должны быть испытаны гидростатическим или манометрическим методом с соблюдением требований СП 72.13130 и сданы по акту представителям технического надзора до производства теплоизоляционных работ. До испытания и теплоизоляции трубопроводов выполнить врезки и закладные детали устройств для приборов КИП и автоматики.

9. Производство работ по монтажу оборудования производить, согласно требованиям производителя..

10. Все проходы через противопожарные стены и перегородки должны быть заделаны сертифицированным герметиком. Места расположения противопожарных стен и перегородок смотреть на архитектурных чертежах.

11. Все оборудование и материалы должны иметь соответствующие сертификаты РФ.

Ведомость рабочих чертежей основного комплекта ОВ5.1

Лист	Наименование	Примечание
01	Общие данные	-
02	План на отм.+0.000. Отопление	-
03	План на отм.+0.000. Кондиционирование воздуха	-
04	План на отм.+0.000. Вентиляция	-
05	Схема системы отпoления	-

Ведомость ссылочных и прилагаемых документов

Обозначение	Наименование	Примечание
ОВ5.1-СО	Спецификация оборудования, изделий и материалов	-


Ведомость основных комплектов марки ОВ

Обозначение	Наименование	Примечание
ОВ1	Здание №02	-
ОВ2	Здание №04	
ОВ3	Здание №01	
ОВ4	Здание №05	
ОВ5.1	Здание №06	
ОВ5.2	Здание №07	

Основные показатели по рабочим чертежам комплекта ОВ2


Наименование здания (сооружения), помещения	Объем, м3	Периоды года при tн, °С	Расход теплоты, Вт				Расход холода, Вт	Установле нная мощность электродви гателей, кВт
			на отопление	на вентиляцию	на горячие водоснабжени е	общий		
Здание №06	-	-17	3960	-	см. проект ВК	3960	-	2.12
	-	+30	-	-	см. проект ВК	-	7800	

						ОВ5.1			
Изм.	Кол.уч	Лист	№док.	Подпись	Дата	Многофункциональный туристический центр "Нихалойские водопады"			
ГИП						Здание № 06	Стадия	Лист	Листов
Разработал		Слюзов					Р	01	
Норм.контр.						Общие данные			
Инв.№			Дог.№						

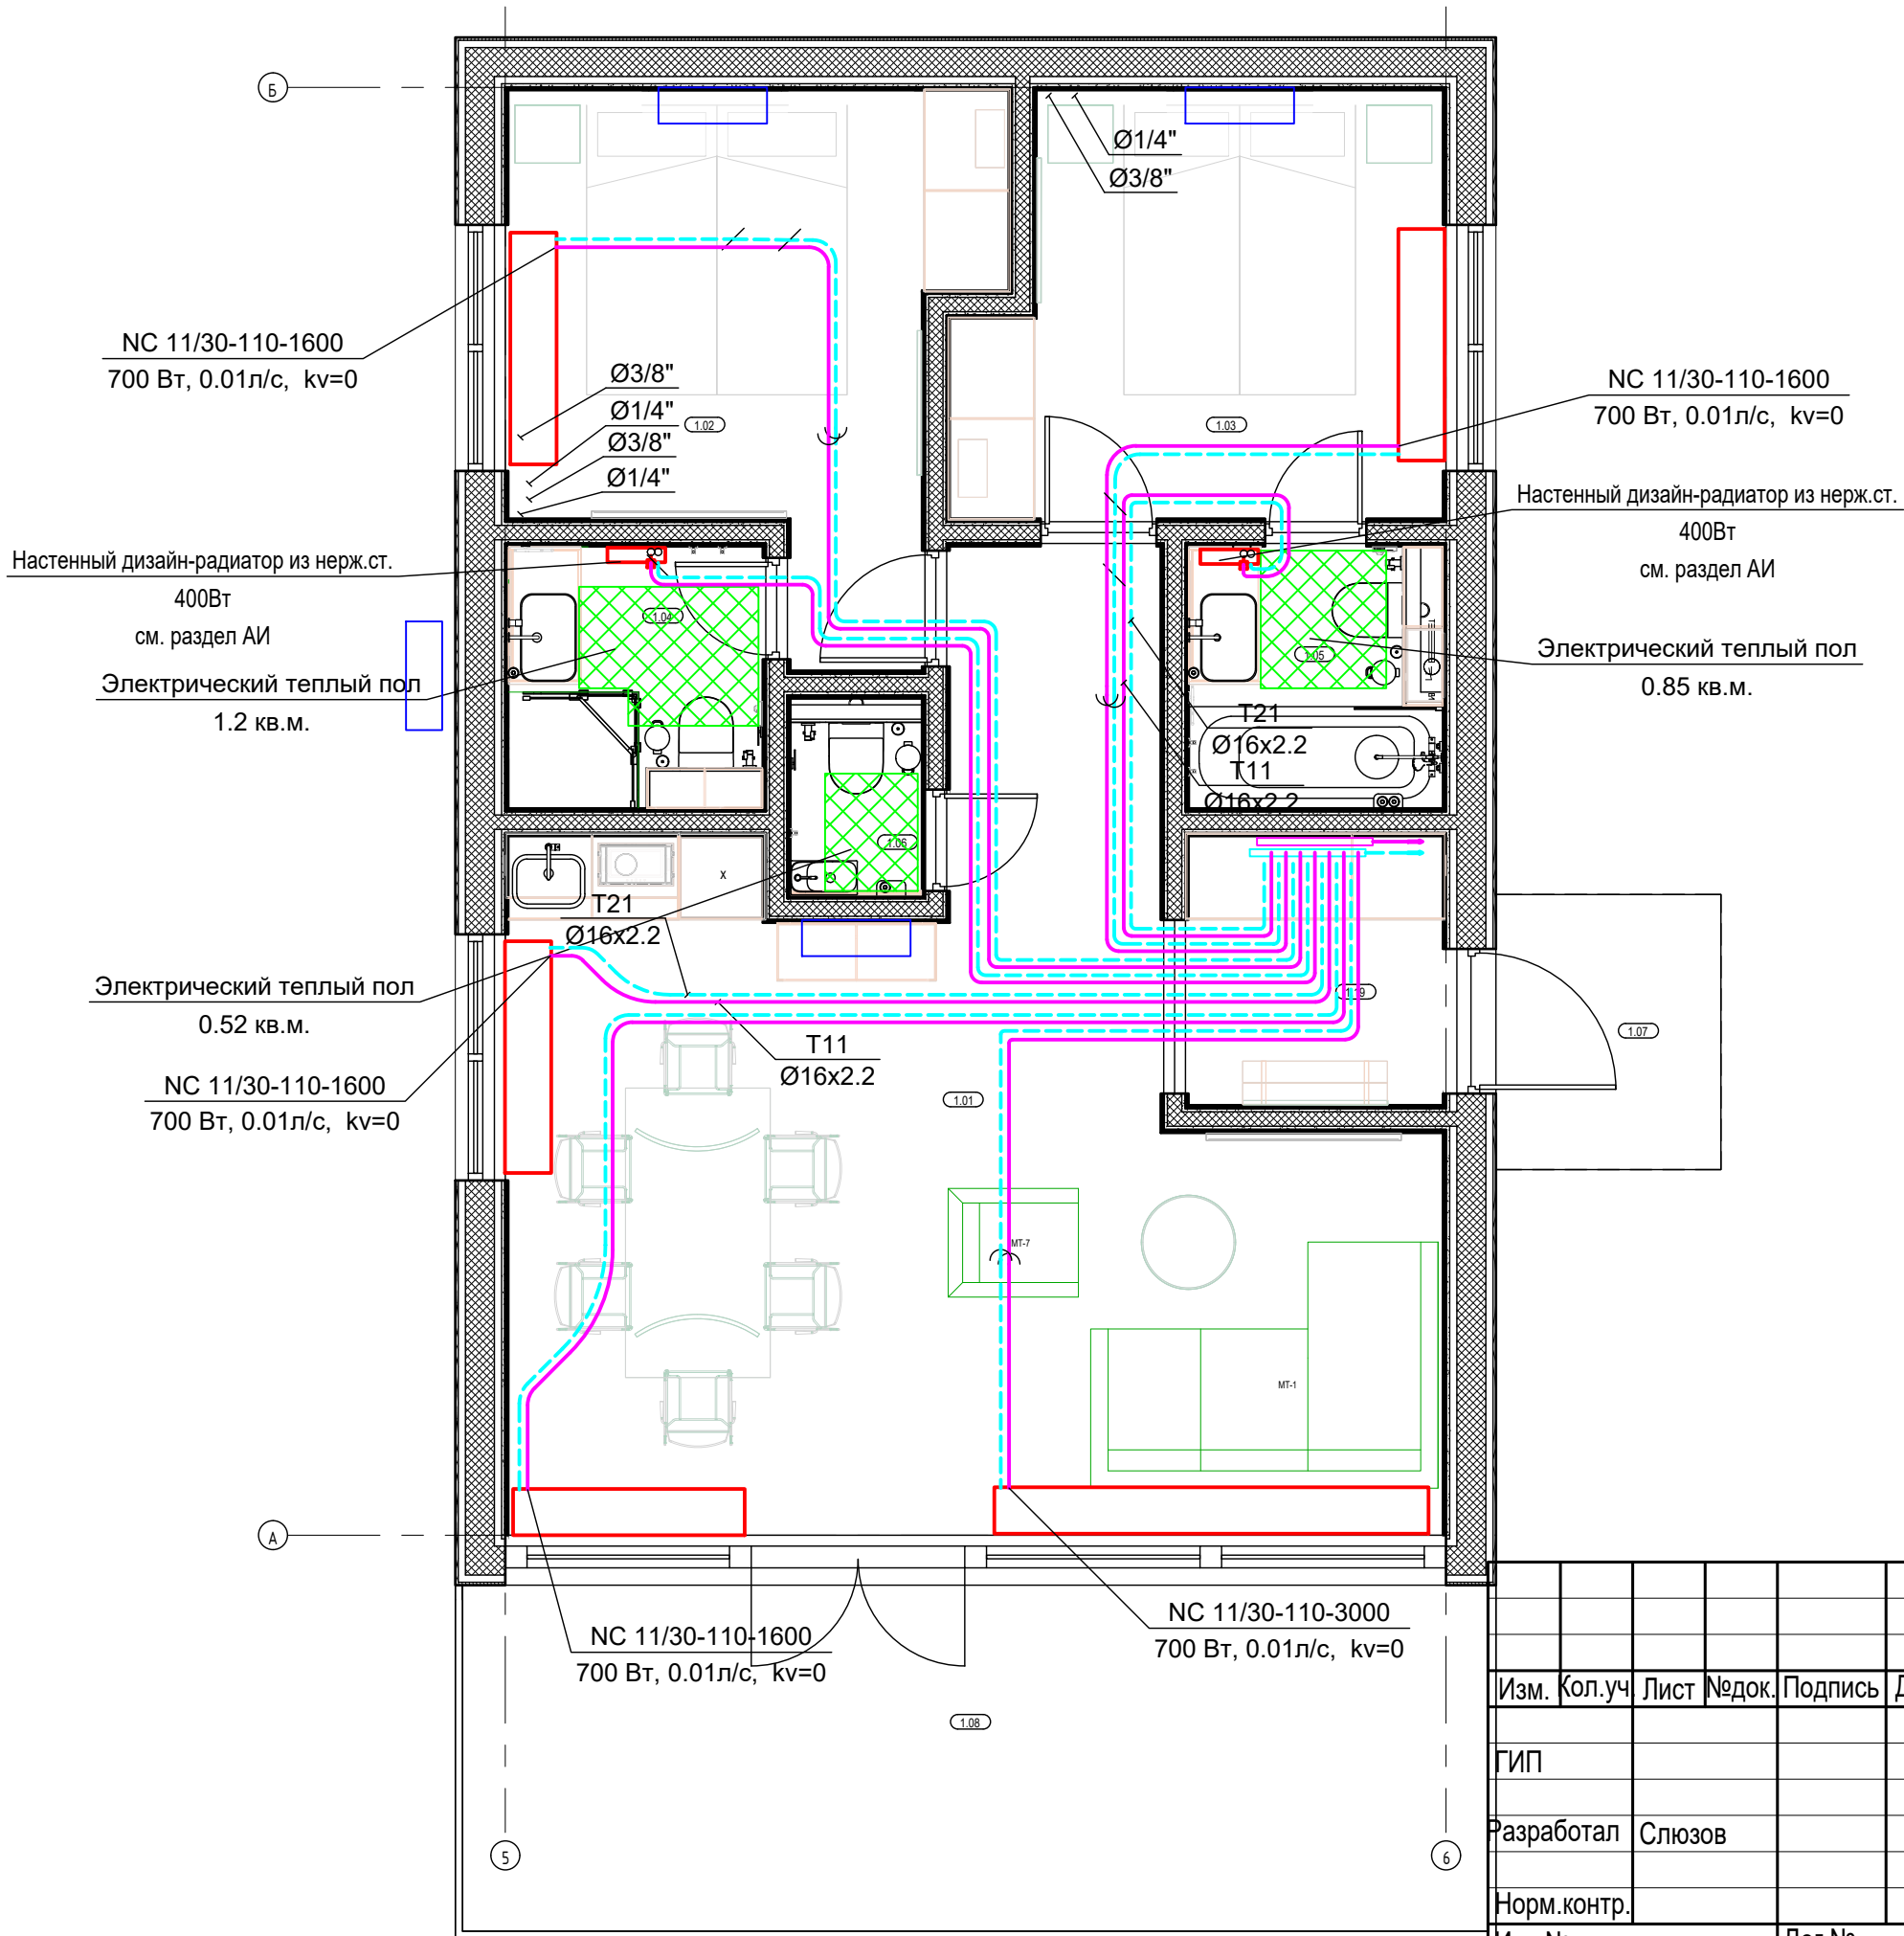

Экспликация помещений			
№	Наименование	Площадь, м2	Кат. пом.
Внутренние помещения			
1.01	Общая комната	30,7	
1.02	Спальная	10,6	
1.03	Спальная	9,4	
1.04	С/У	3,3	
1.05	С/У	3,3	
1.06	С/У	1,3	
1.19	Тамбур	3,4	
		62	


						ОВ5.1			
Изм.	Кол.уч	Лист	№ док.	Подпись	Дата	Многофункциональный туристический центр "Нихалойские водопады"			
ГИП						Здание № 06	Стадия	Лист	Листов
Разработал		Слюзов					Р	02	
Норм.контр.						План на отм.+0.000. Отопление			
Инв.№			Дог.№						

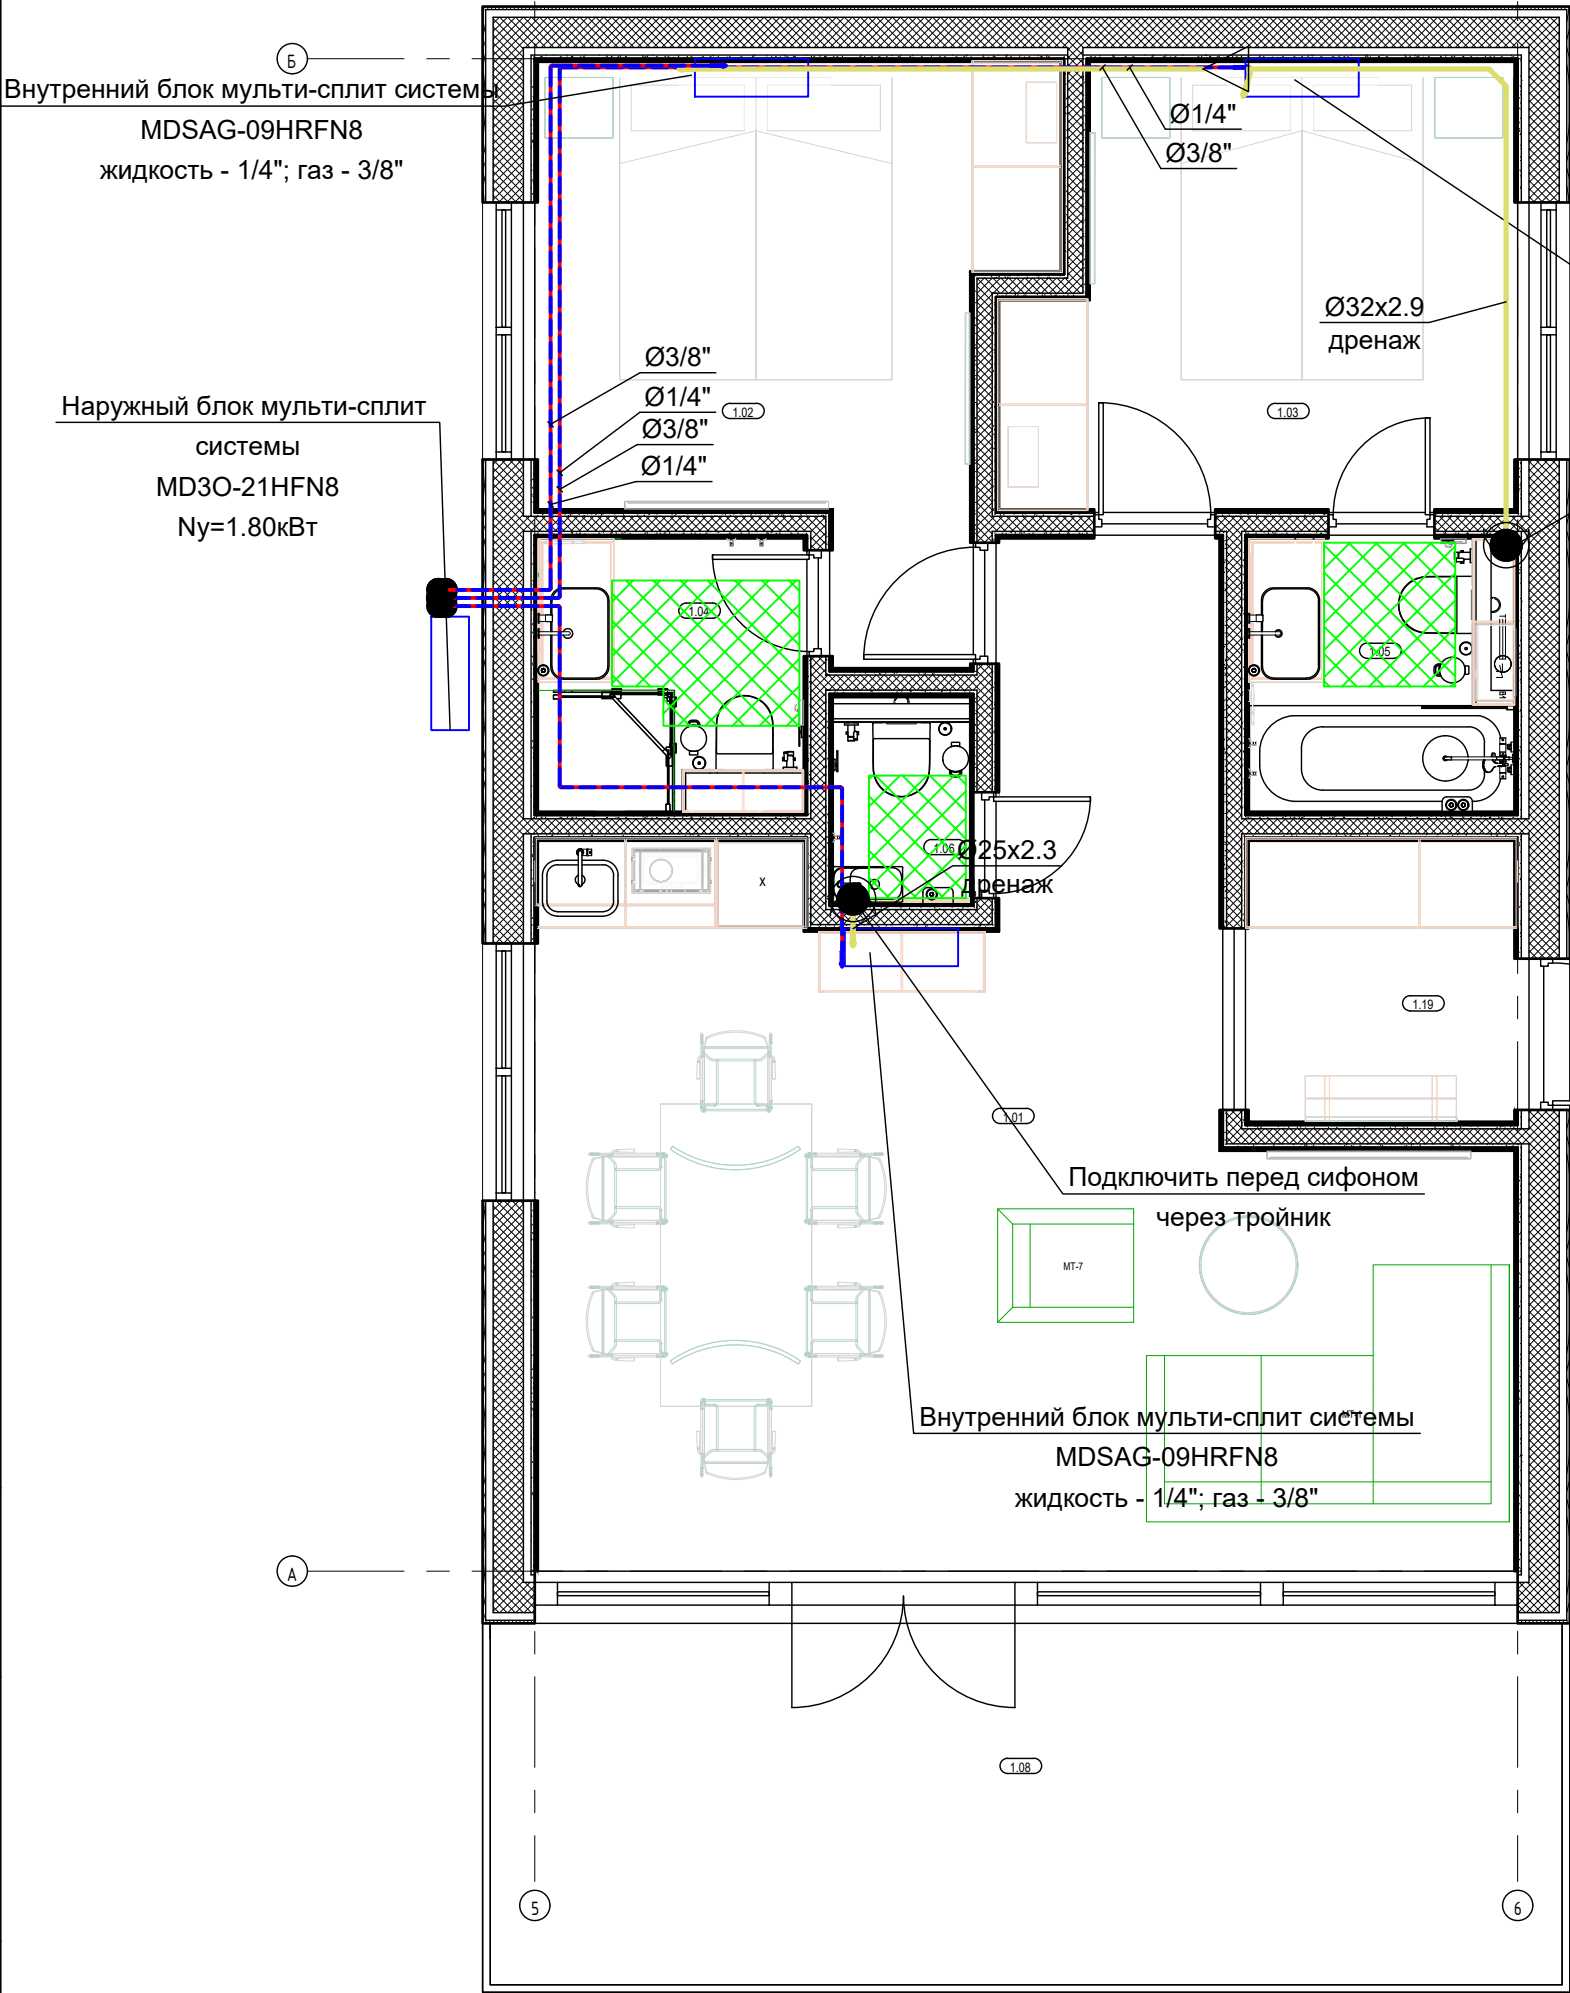

Экспликация помещений			
№	Наименование	Площадь, м2	Кат. пом.
Внутренние помещения			
1.01	Общая комната	30,7	
1.02	Спальная	10,6	
1.03	Спальная	9,4	
1.04	СС/У	3,3	
1.05	СС/У	3,3	
1.06	С/У	1,3	
1.19	Тамбур	3,4	
		62	

- Примечания:
1. Трубопроводы показаны условно. Привязки и отметки уточняются при выполнении монтажных работ с учетом дизайн-проекта;
 2. Дренажные трубопроводы проложить с уклоном не менее 0.01 от внутреннего блока к стояку;
 3. Фреоноводы и дренажные трубопроводы проложить в конструкции перегородки или штробе;
 4. Дренажные трубопроводы подключить к системе бытовой канализации, если не указано иное подключение, через капельные воронки с сухим затвором (см. раздел ВК);

						ОВ5.1			
Изм.	Кол.уч.	Лист	№ док.	Подпись	Дата	Многофункциональный туристический центр "Нихалойские водопады"			
ГИП						Здание № 06	Стадия	Лист	Листов
Разработал	Слюзов						Р	03	
Норм.контр.						План на отм. +0.000. Кондиционирование воздуха			
Инв.№			Дог.№						

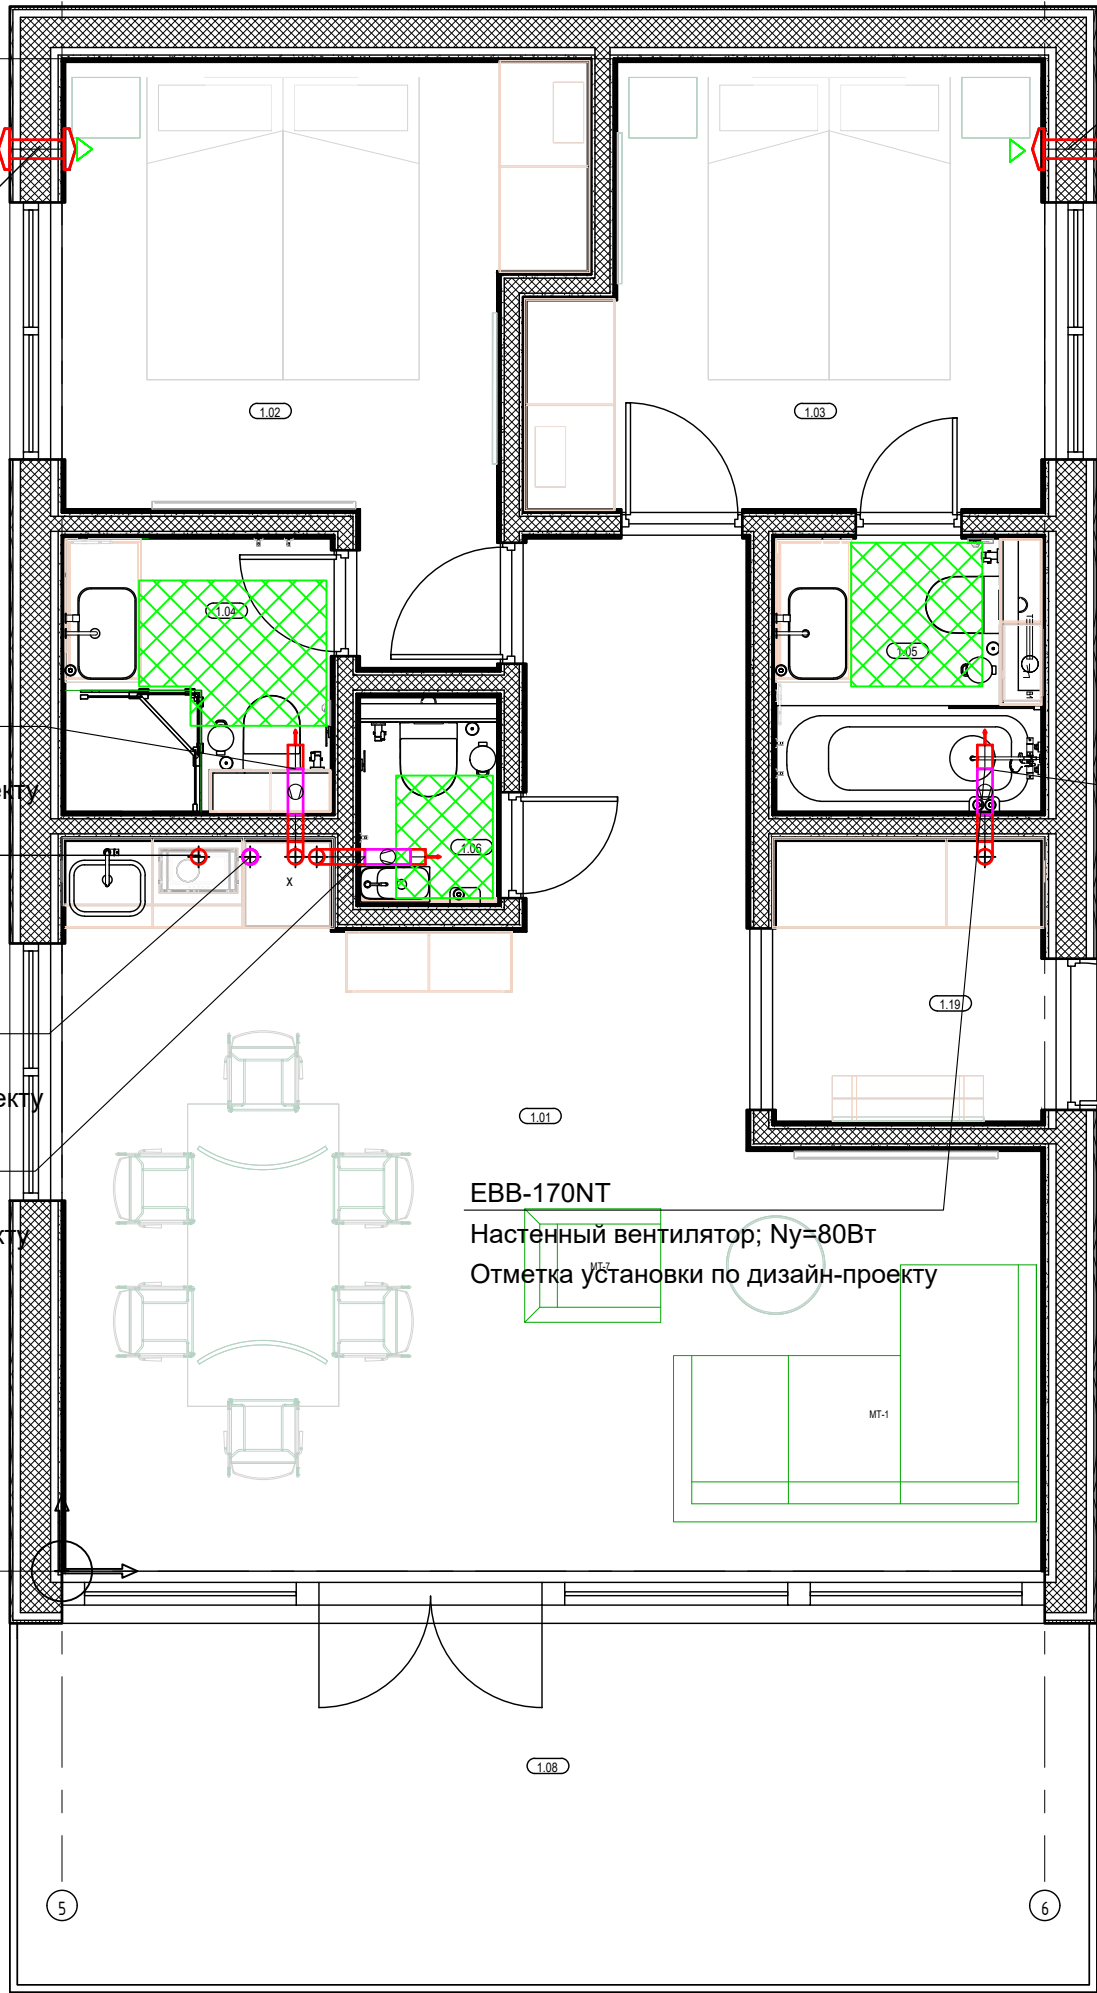

Бризер SILEM KITHY 125
отм. не менее +2400 от у.ч.п.

Бризер SILEM KITHY 125
отм. не менее +2400 от у.ч.п.

EBB-170NT
Настенный вентилятор; Nu=80Вт
Отметка установки по дизайн-проекту
Ø100

Подключение кухонной вытяжки
Обратный клапан в составе
вытяжки в проекте не учтен

EBB-170NT
Настенный вентилятор; Nu=80Вт
Отметка установки по дизайн-проекту

EBB-170NT
Настенный вентилятор; Nu=80Вт
Отметка установки по дизайн-проекту

EBB-170NT
Настенный вентилятор; Nu=80Вт
Отметка установки по дизайн-проекту

EBB-170NT
Настенный вентилятор; Nu=80Вт
Отметка установки по дизайн-проекту

Экспликация помещений

№	Наименование	Площадь, м2	Кат. пом.
Внутренние помещения			
1.01	Общая комната	30,7	
1.02	Спальная	10,6	
1.03	Спальная	9,4	
1.04	С/У	3,3	
1.05	С/У	3,3	
1.06	С/У	1,3	
1.19	Тамбур	3,4	

62

ОВ5.1

Многофункциональный туристический центр "Нихалойские водопады"

Здание № 06

Стадия	Лист	Листов
Р	04	

План на отм.+0.000. Вентиляция

Позиция	Наименование и техническая характеристика	Тип, марка, обозначение документа, опросного листа	Код оборудования, изделия, материала	Завод- изготовитель	Единица измерения	Количество	Масса ед. кг	Примечания
1	2	3	4	5	6	7	8	9
	Отопление							
1.	Конвектор внутипольный с естественной конвекцией, в комплекте с присоединительной грнитурой	SPL-NC-11/30-1600		SPL	шт.	5		
2.	Конвектор внутипольный с естественной конвекцией, в комплекте с присоединительной грнитурой	SPL-NC-11/30-3000		SPL	шт.	1		
3.	Коллекторная группа	SPL-DCU-BV-CS50-7R-20-R20R-P20R-B15R		SPL	Компл.	1		
4.	Труба из сшитого полиэтилена 16x2.2			SPL	п.м.	120		
5.	Трубка теплоизолирующая Ф16, толщина 6мм	ПУ-Флекс		ПУ-Флекс	п.м.	120		
	Вентиляция							
6.	Вентилятор бытовой настенный со встроенным таймером	EBB-170NT		Soler&palau	шт.	4		
7.	Металлический крышный зонт	СТ-125 TEJA		Soler&palau	шт.	5		
8.	Воздуховод из оцинкованной стали толщиной 0.5 мм	Ф100			п.м.	8		
9.	Отвод из оцинкованной стали толщиной 0.5 мм	Ф100			шт.	3		
10.	Переход из оцинкованной стали толщиной 0.5 мм	Ф100/Ф125			шт.	5		
11.	Гигрорегулируемый приточный клапан	SILEM KIT HY 125		Soler&palau	шт.	2		
12.	Теплоизоляция из вспененного каучука	ПУ-Флекс		ПУ-Флекс	кв.м.	3		
13.	Крепежные элементы				кг.	15		Уточняется при монтаже
	Кондиционирование воздуха							
14.	Наружный блок мультисплит системы	MD3O-21HFN8		MDV	шт.	1		
15.	Внутренний блок мультисплит системы	MDSAG-09HRFN8		MDV	шт.	3		
16.	Труба медная 1/4"				п.м.	26		
17.	Труба медная 3/8"				п.м.	26		
18.	Трубка теплоизолирующая 1/4", толщина 16мм	ПУ-Флекс		ПУ-Флекс	п.м.	26		
19.	Трубка теплоизолирующая 3/8", толщина 16мм	ПУ-Флекс		ПУ-Флекс	п.м.	26		
20.	Труба полипропиленовая Ф25х2.3	PP-R SDR11		Proaqua	п.м.	17		

Изм.

Кол.

Лист

№д

Подпись

Дата

Отопление, вентиляция и кондиционирование воздуха

Стадия

Лист

Листов

Р

1

1

Н. контроль

Инв. №

Дог.№

Спецификация оборудования, изделий и материалов.