
Схема системы В 1

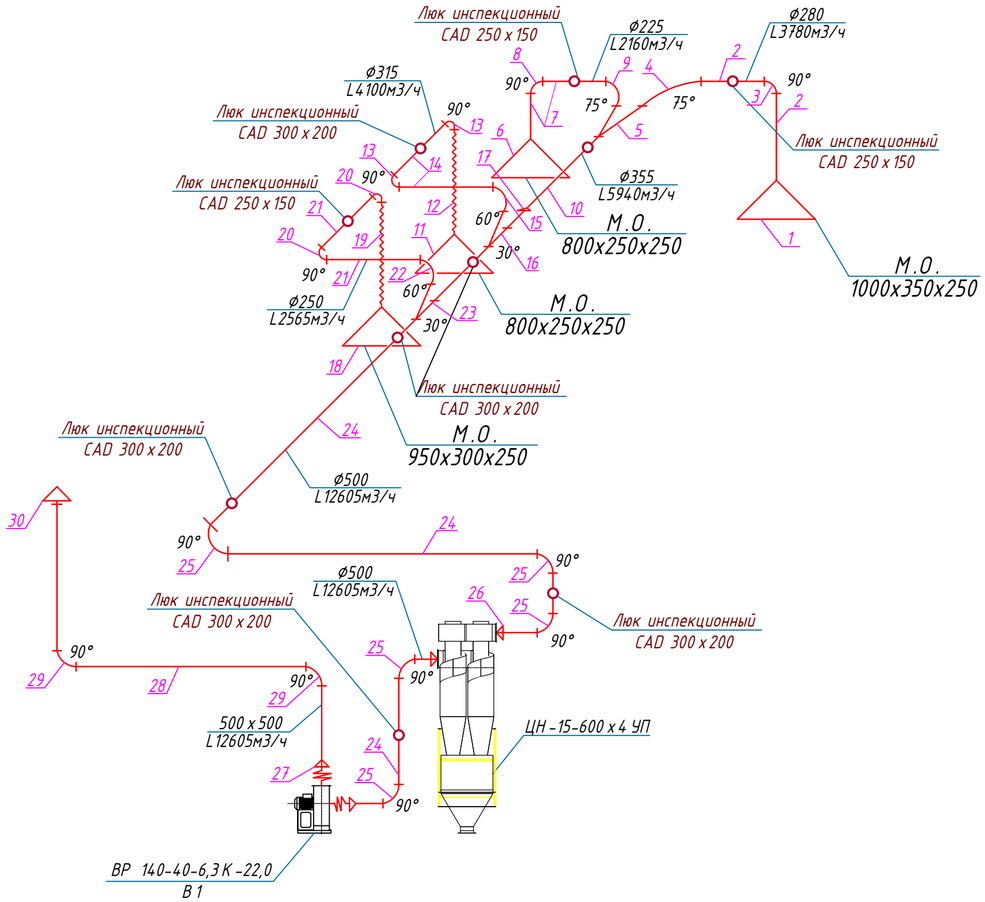

Спецификация изделий и материалов

Поз. обозначение	Наименование	Кол.	Примечание
1	Местный отсос 1000x350x250(h) мм	1	
2	Прямик D=280 мм; L=1250 мм	4	
3	Отвод ∠ 90°; R=560 мм; D=280 мм	1	
4	Отвод ∠ 75°; R=560 мм; D=280 мм	1	
5	Тройник D355/D225/D280	1	
6	Местный отсос 800x250x250(h) мм	1	
7	Прямик D=225 мм; L=1250 мм	4	
8	Отвод ∠ 90°; R=450 мм; D=225 мм	1	
9	Отвод ∠ 75°; R=450 мм; D=225 мм	1	
10	Прямик D=355 мм; L=1250 мм	3	
11	Местный отсос 800x250x250(h) мм	1	
12	Воздуховод полиуретановый PUR FR1.0, диам. 315 мм	1	(3 метра)
13	Отвод ∠ 90°; R=630 мм; D=315 мм	2	
14	Прямик D=315 мм; L=1250 мм	4	
15	Отвод ∠ 60°; R=630 мм; D=315 мм	1	
16	Тройник 500/315/500	1	
17	Переходник D500/D355	1	
18	Местный отсос 950x300x250(h) мм	1	
19	Воздуховод полиуретановый PUR FR1.0, диам. 250 мм	1	(3 метра) "Юнифлекс"
20	Отвод ∠ 90°; R=500 мм; D=250 мм	2	
21	Прямик D=250 мм; L=1250 мм	4	
22	Отвод ∠ 60°; R=500 мм; D=250 мм	1	
23	Тройник 500/250/500	1	
24	Прямик D=500 мм; L=1250 мм	22	
25	Отвод ∠ 90°; R=1000 мм; D=500 мм	7	
26	Переходник 672x396/D500	1	
27	Переходник 378x378/500x500	1	
28	Прямик 500x500 мм; L=1250 мм	18	
29	Отвод ∠ 90°; 500x500 мм	1	
30	Зонт вентиляционный круглый D500	1	

Согласовано

Взам. инв. №

Подп. и дата

Инв. № подл.

Изм.	Кол. уч.	Лист	№ док.	Подп.	Дата	25/03-Р-ОВ			
						Система аспирации прессового участка и участка садки кирпича в производственном цехе на объекте, по адресу: г. Ростов-на-Дону, ул. Курская, д. 186.			
Исполн.		Иванов			04.26	Производственный цех.	Стадия	Лист	Листов
ГИП		Салагаева			04.26		Р	2	
Н. контр.		Панчев			04.26				
						Система В1.	ООО "Проминжиниринг"		

Формат