


Спецификация изделий и материалов

Поз. обозна-чение	Наименование	Кол.	Примечание
1	Местный отсос 1900х250х250(н) мм	1	
2	Прямик D=200 мм; L=1250 мм	4	
3	Отвод ∠ 90°; R=400 мм; D=200 мм	1	
4	Переходник D280/D200	1	
5	Отвод ∠ 60°; R=400 мм; D=200 мм	2	
6	Тройник D280/D200/D200	1	
7	Переходник D355/D280	1	
8	Тройник D355/D200/D280	1	
9	Прямик D=280 мм; L=1250 мм	1	
10	Прямик D=355 мм; L=1250 мм	8	
11	Отвод ∠ 90°; R=710 мм; D=355 мм	3	
12	Местный отсос 800х300х400(н) мм	1	
13	Прямик D=225 мм; L=1250 мм	6	
14	Отвод ∠ 90°; R=450 мм; D=225 мм	1	
15	Отвод ∠ 60°; R=450 мм; D=225 мм	1	
16	Тройник D400/D225/D355	1	
17	Прямик D=400 мм; L=1250 мм	32	
18	Отвод ∠ 90°; R=800 мм; D=400 мм	4	
19	Прямик 400х400 мм; L=1250 мм	8	
20	Переходник 336х396/D400	1	
21	Переходник 378х378/400х400	1	
22	Переходник D500/D400	1	
23	Зонт вентиляционный прямоугольный 400х400 мм	1	

Схема системы В 2

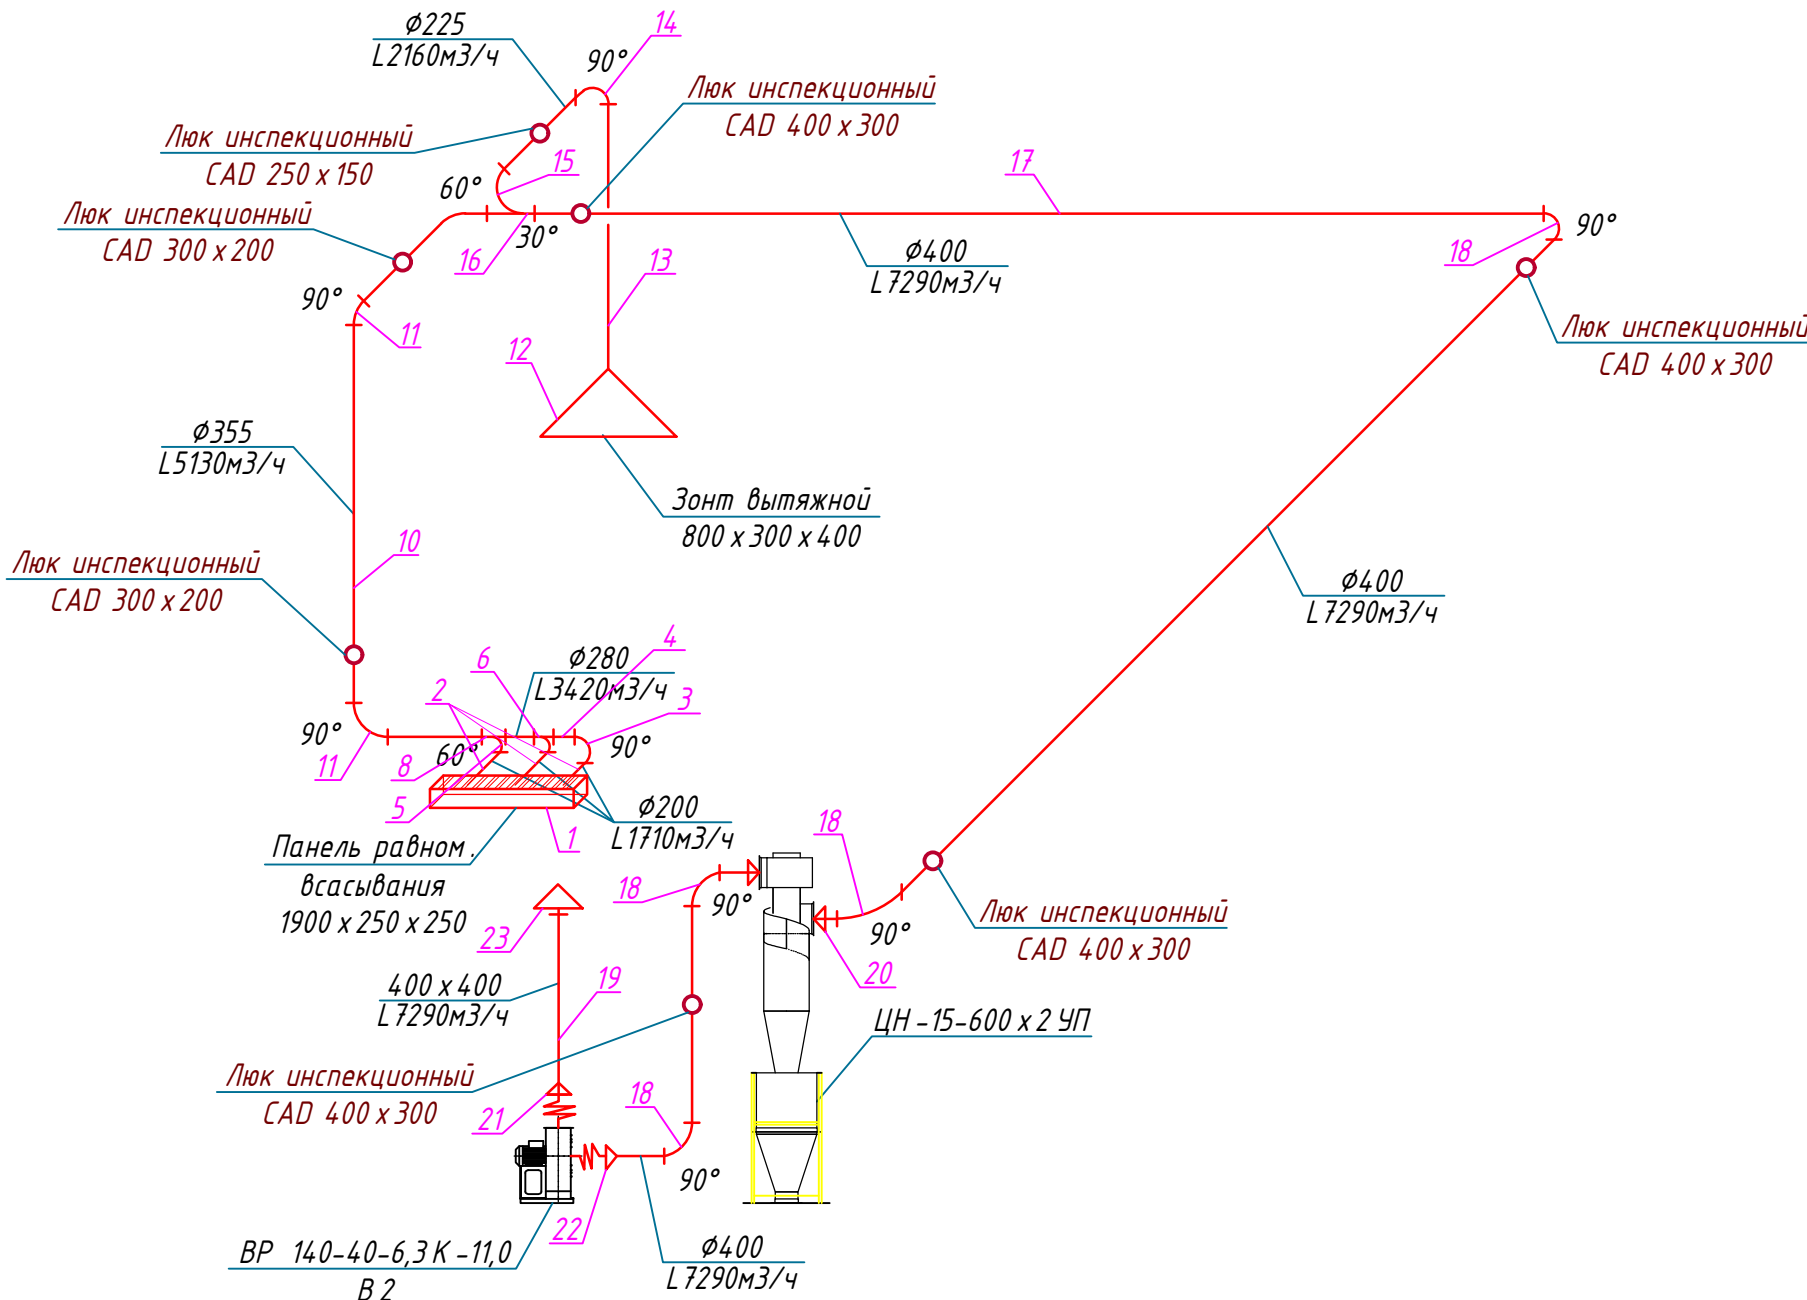

Согласовано

Взам. инв. №

Подп. и дата

Инв. № подл.

							25/03-Р-ОВ
							Система аспирации прессового участка и участка садки кирпича в производственном цехе на объекте, по адресу: г. Ростов-на-Дону, ул. Курская, д. 188.
Изм.	Кол. уч.	Лист	№ док	Подп.	Дата		
Исполн.	Иванов				04.26		
ГИП	Салагаева				04.26	Производственный цех.	Р
Н. контр.	Панчев				04.26		З
						Система В2.	000 "Проминжендинг"